


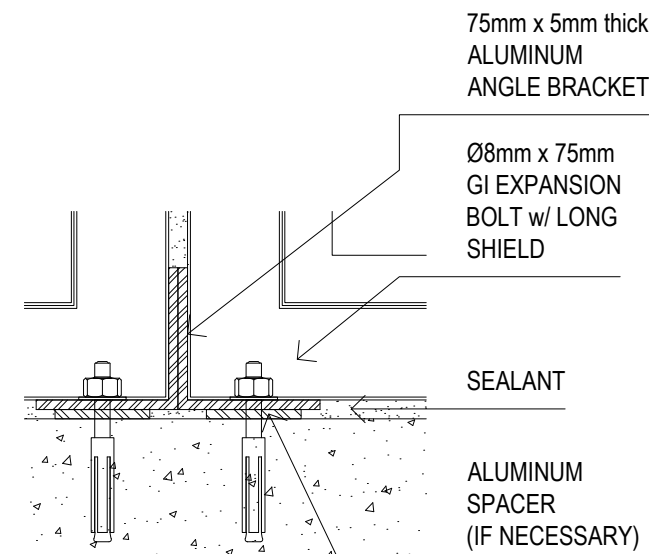


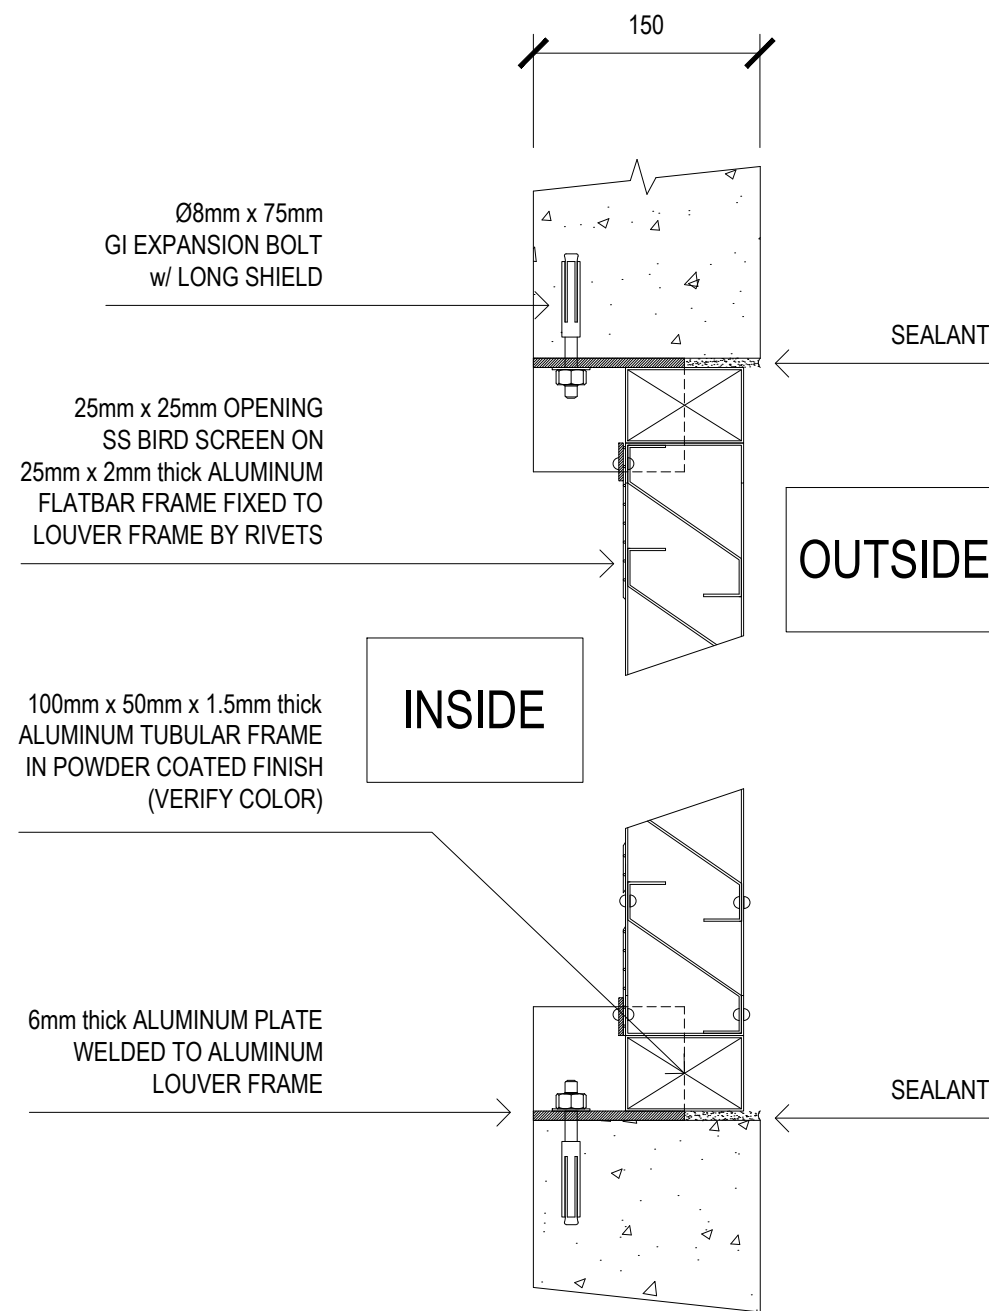

ALUMINUM LOUVER
BLOW-UP 01
SCALE 1:04

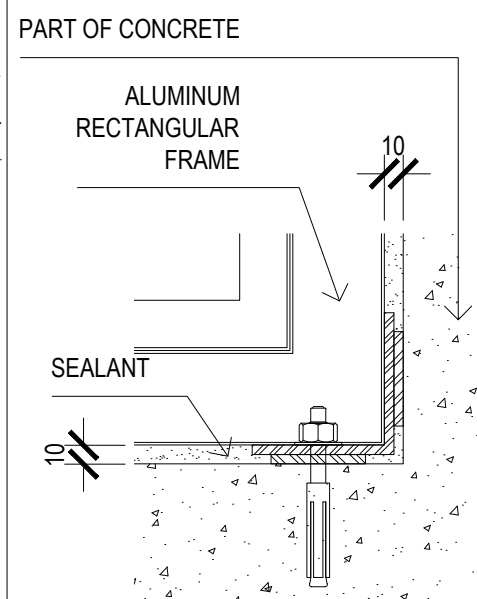


ALUMINUM LOUVER
BLOW-UP 02
SCALE 1:04

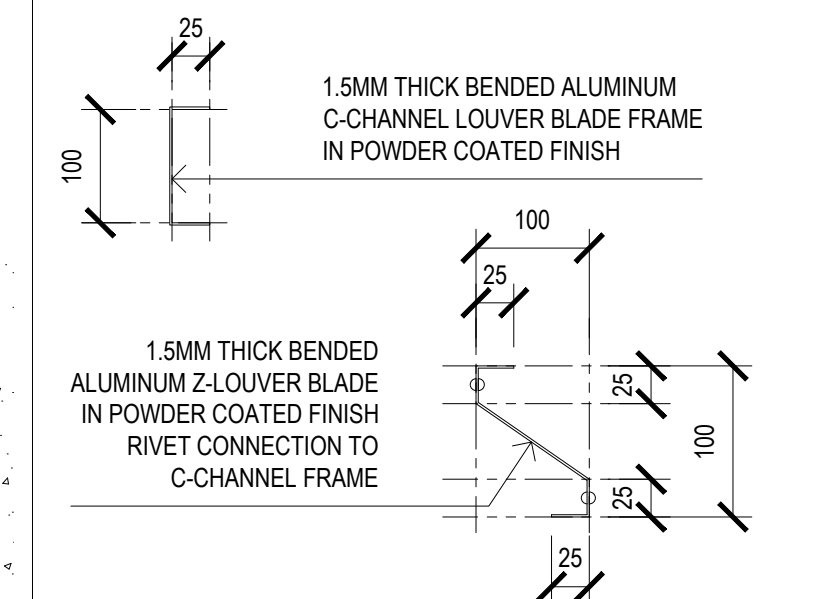

ALUMINUM LOUVER
CHANNEL & BLADE PROFILE
SCALE 1:05

ALUMINUM LOUVER
LOUVER DETAILED SECTION TYP.
SCALE NTS

- NOTES:
1. ALL DIMENSIONS ARE IN MILLIMETERS
 2. SUBJECT FOR FINAL SITE INSPECTION AND ACTUAL MEASUREMENT BEFORE FABRICATION
 3. ALL ALUMINUM MEMBERS ARE IN POWDER COATED FINISH

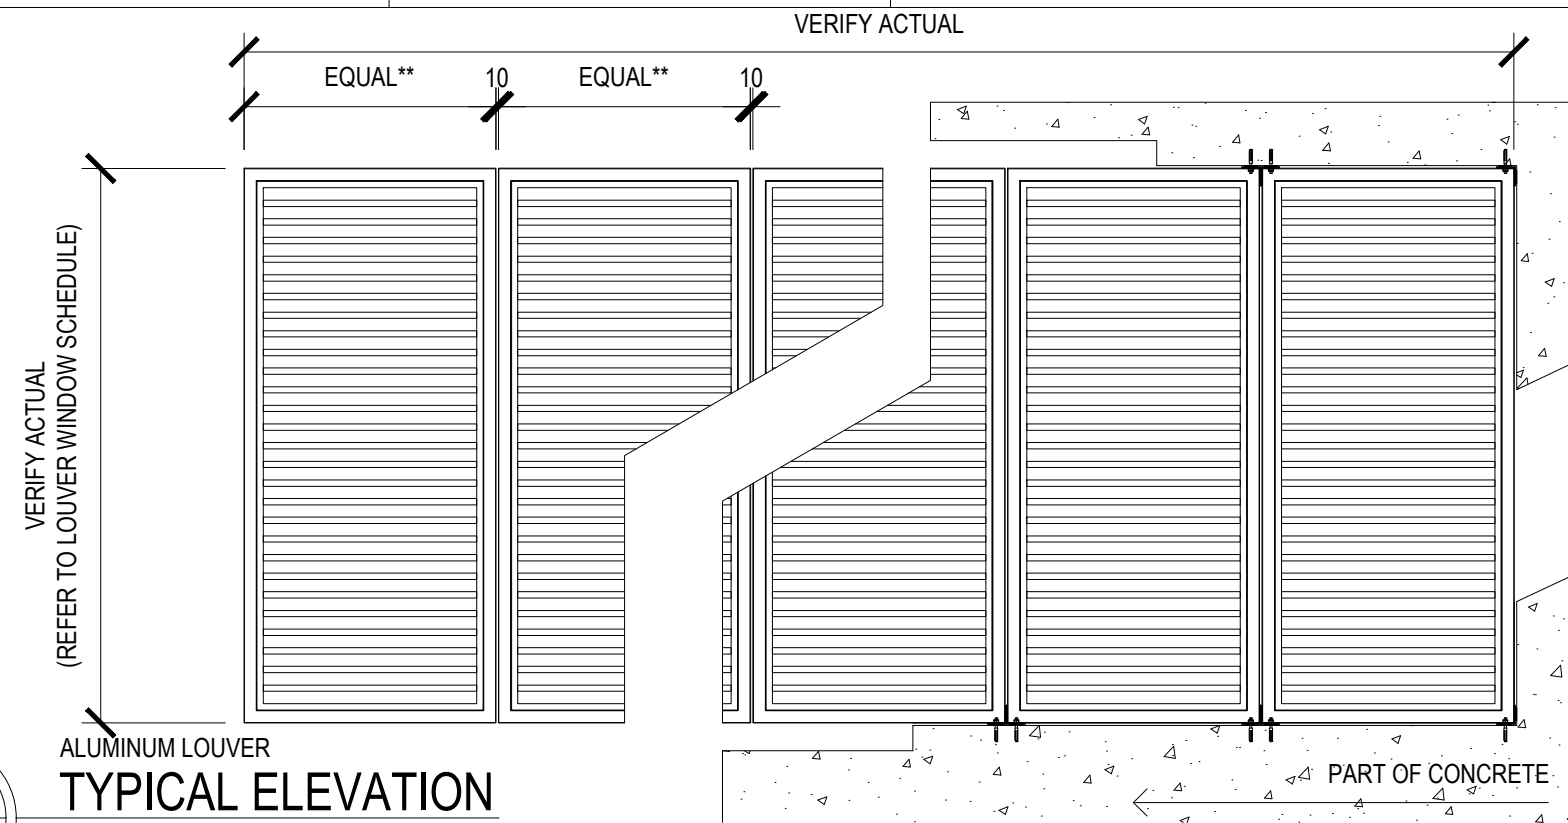

ALUMINUM LOUVER
TYPICAL ELEVATION
SCALE 1:30



ORO FILIPINO
ENTERPRISES & DEVELOPMENT CORP.
Rm. 217 HILLCREST CONDOMINIUM 1616 E. RODRIGUEZ SR. AVE.,
QUEZON CITY, PHILIPPINES
TEL. NOS. 416-4557 570-7544 570-7705 570-8312
FAX NO. 414-3146 EMAIL: engineering@orofilipino.co

PROJECT TITLE:
SUNSHINE FORT PROJECT
LOCATION: 8TH AVENUE FORT BONIFACIO NCBD TAGUIG CITY

OWNER/DEVELOPER:
FEDERAL LAND INC.

GENERAL CONTRACTOR:
EEI CORPORATION

SHEET CONTENT:
**ALUMINUM LOUVER
TYPICAL DETAILS**
REMARKS:

SHEET NUMBER:
1.00
REVISION: 2.00