


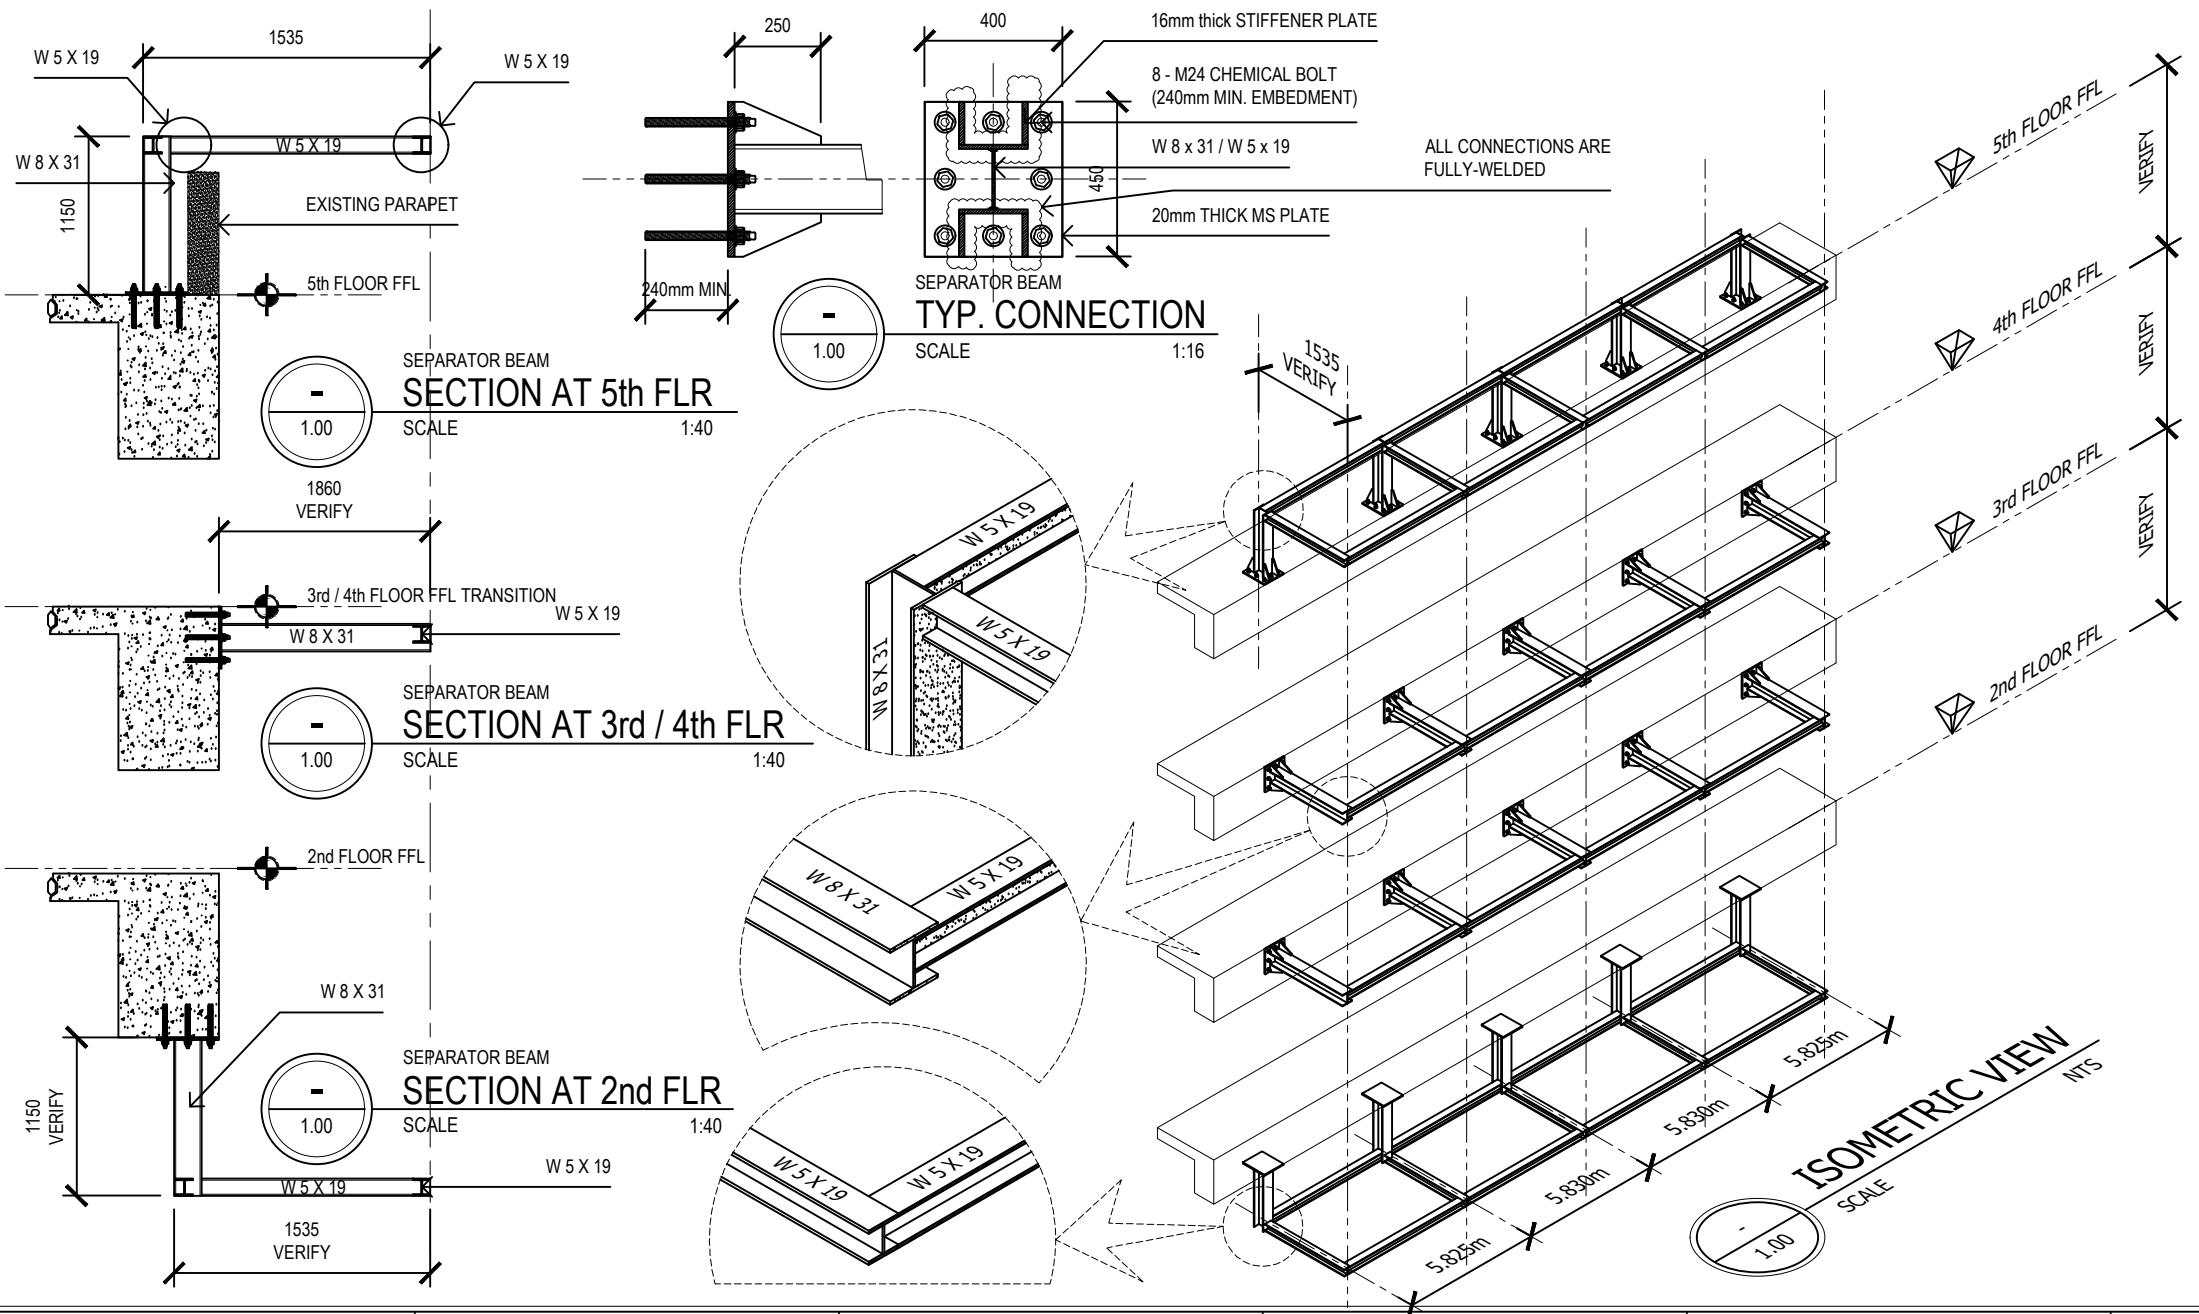

ORO FILIPINO
ENTERPRISES & DEVELOPMENT CORP.
Rm. 217 HILLCREST CONDOMINIUM 1616 E. RODRIGUEZ SR. AVE.,
QUEZON CITY, PHILIPPINES
TEL NOS. 416-4557 570-7544 570-7705 570-8312
FAX NO. 414-3146 EMAIL: engineering@orofilipino.co

PROJECT TITLE:
**PARK TRIANGLE RESIDENCES
PROJECT FORCE LIGHTSABER**

LOCATION: 32nd street corner 11th avenue, Bonifacio Global City, Taguig City, Philippines

OWNER/DEVELOPER:
MAKATI DEVELOPMENT CORPORATION

GENERAL CONTRACTOR:
MAKATI DEVELOPMENT CORPORATION

SHEET CONTENT:
EIFS SUPPORT

REMARKS:

SHEET NUMBER
1.00