


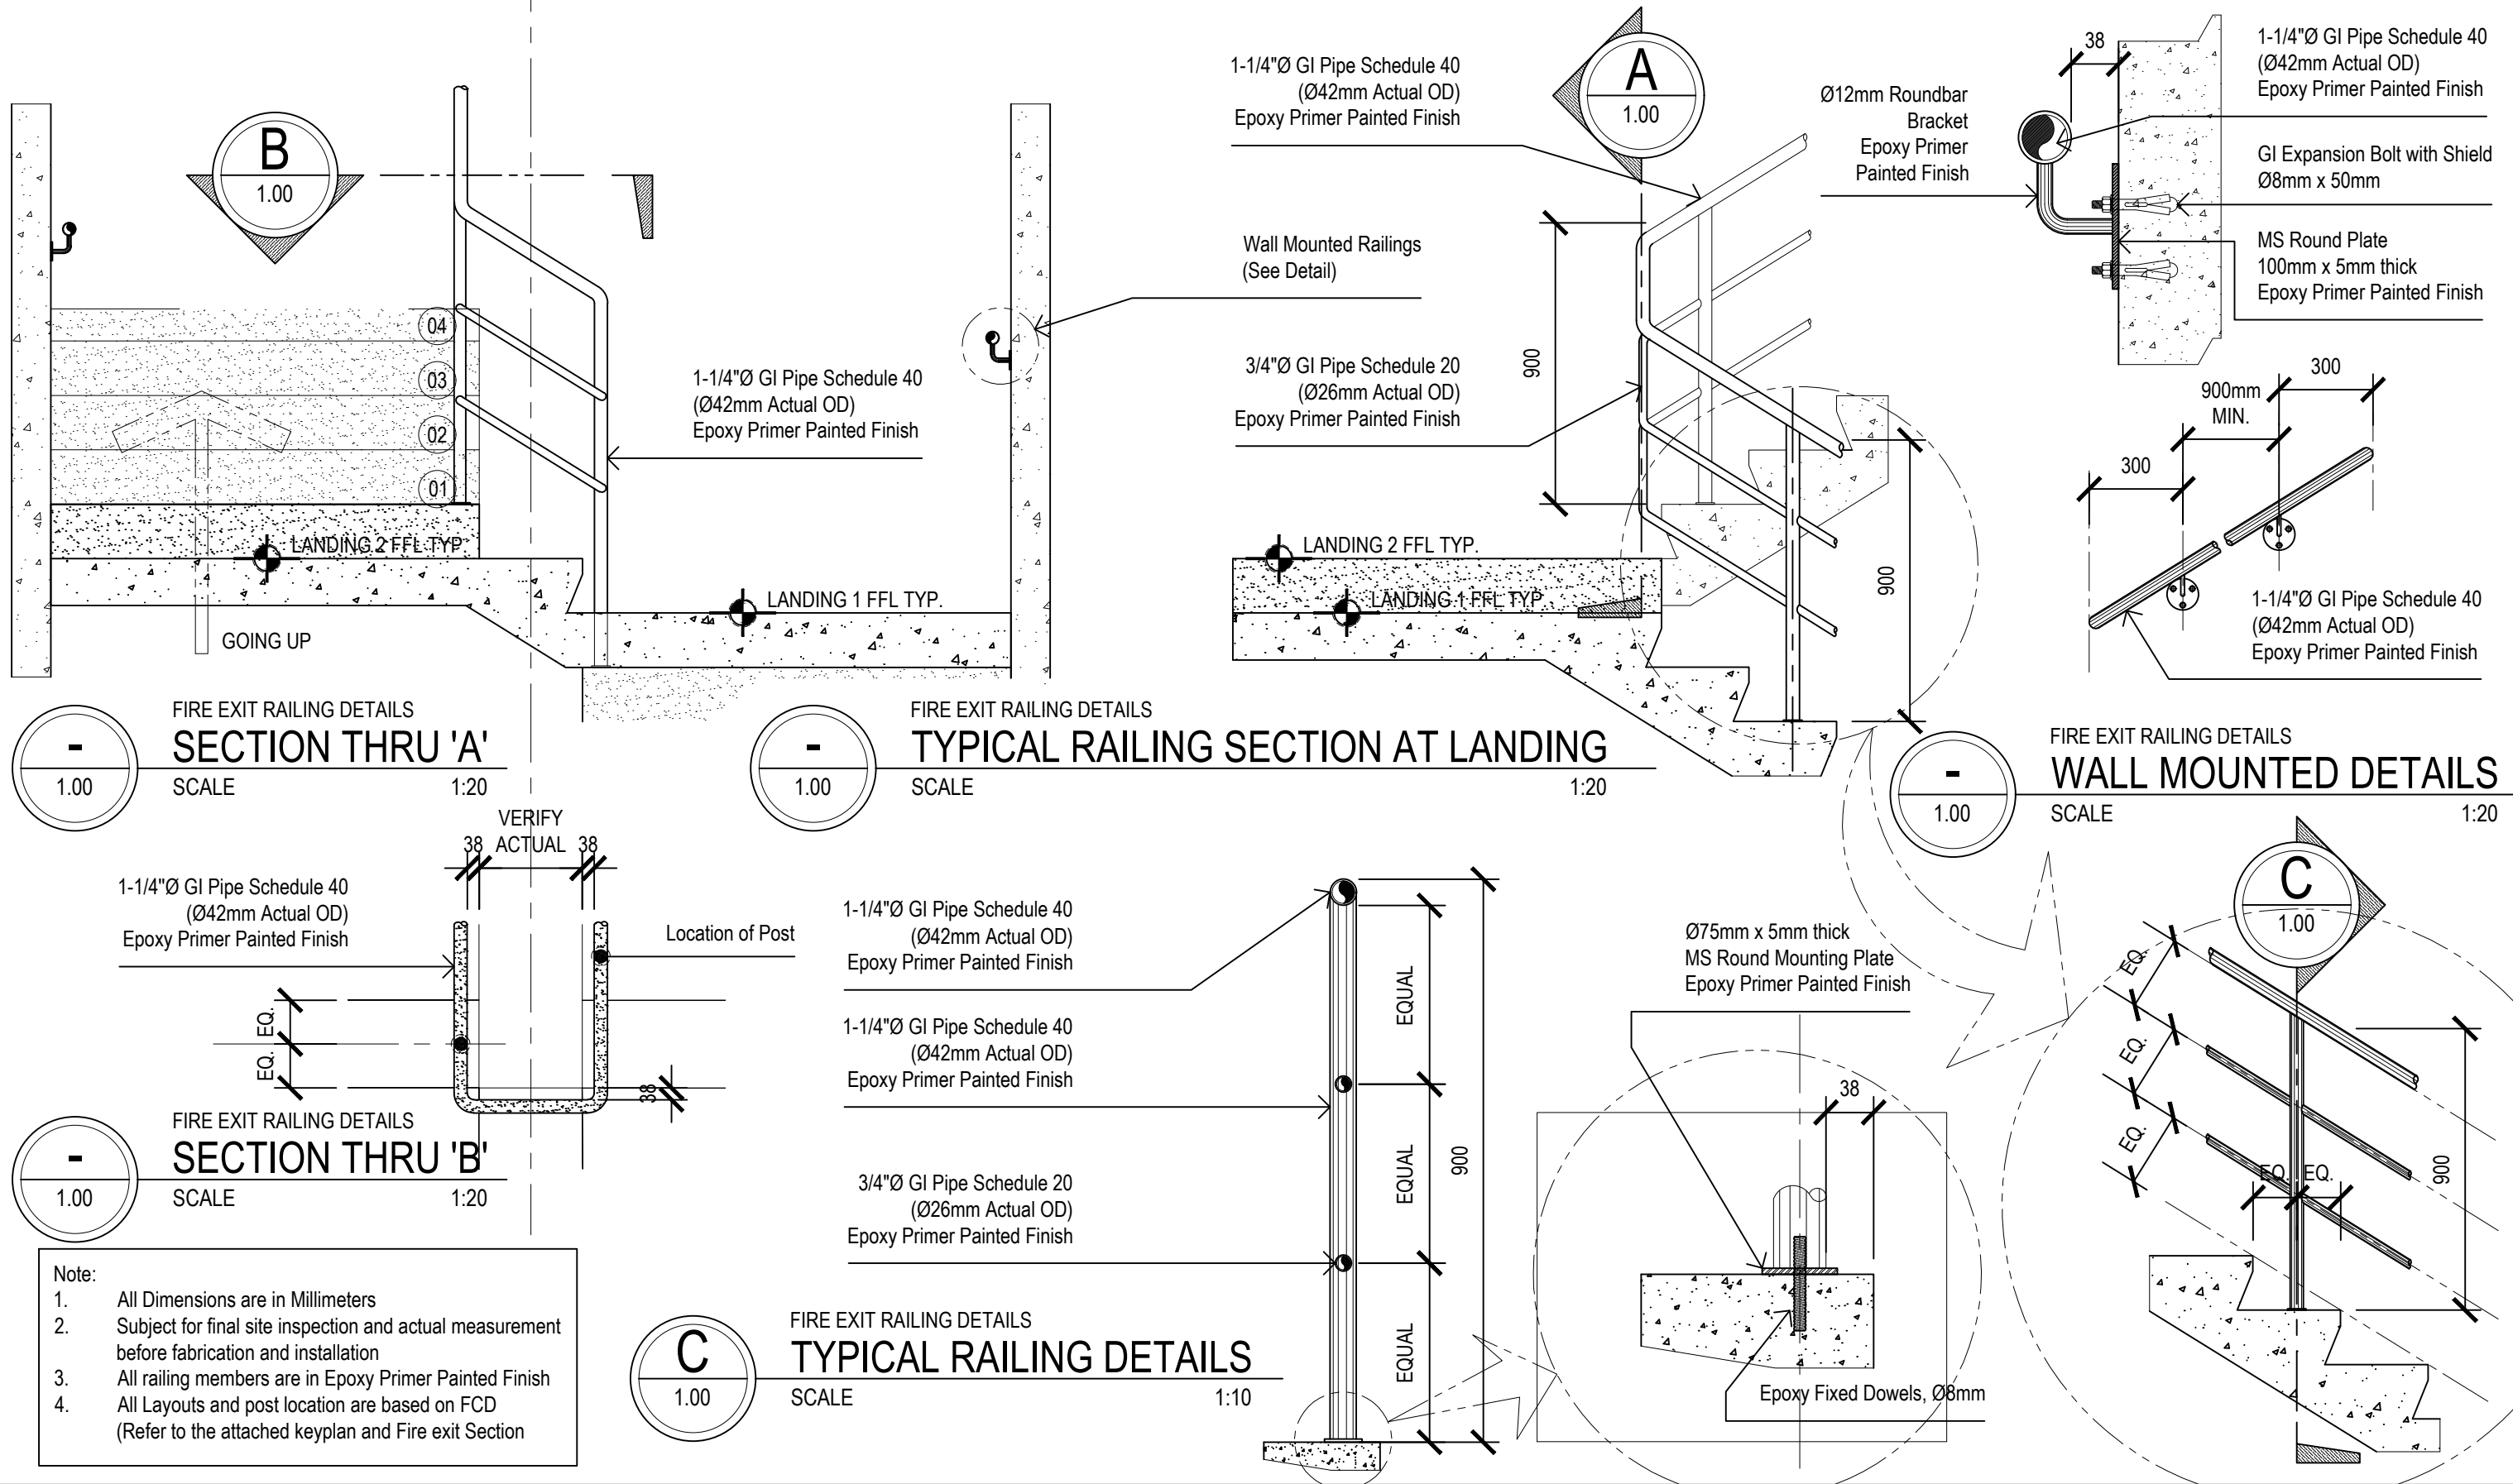

	PROJECT TITLE:	OWNER/DEVELOPER:	GENERAL CONTRACTOR:	SHEET CONTENT:	SHEET NUMBER:
				FIRE EXIT RAILING DETAILS (Floor & Wall Mounted Railings)	1.00
				REMARKS:	REVISION: 0.0