




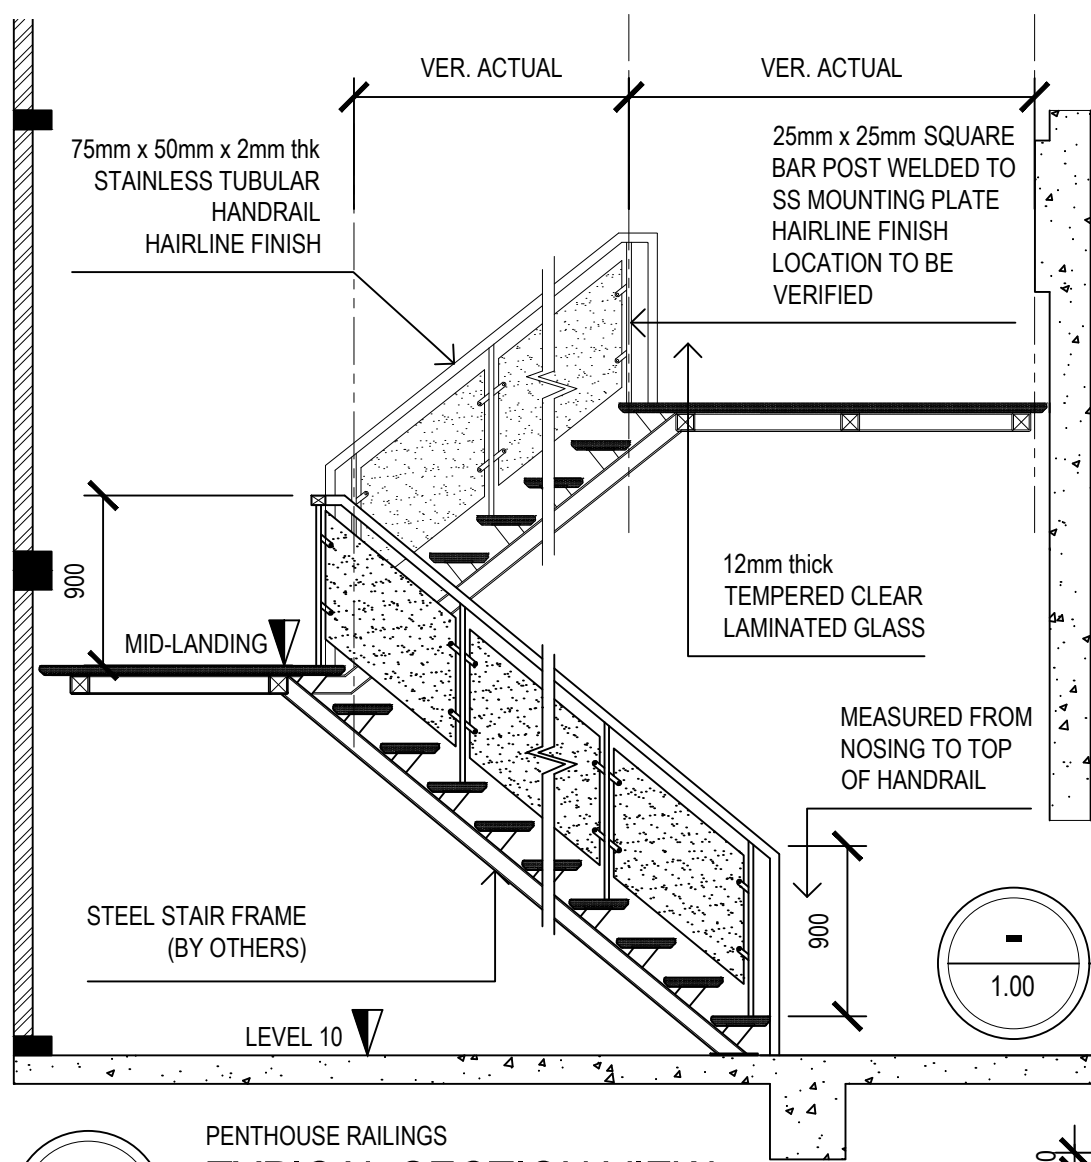


PENTHOUSE RAILINGS
TYPICAL SECTION VIEW
SCALE 1:40

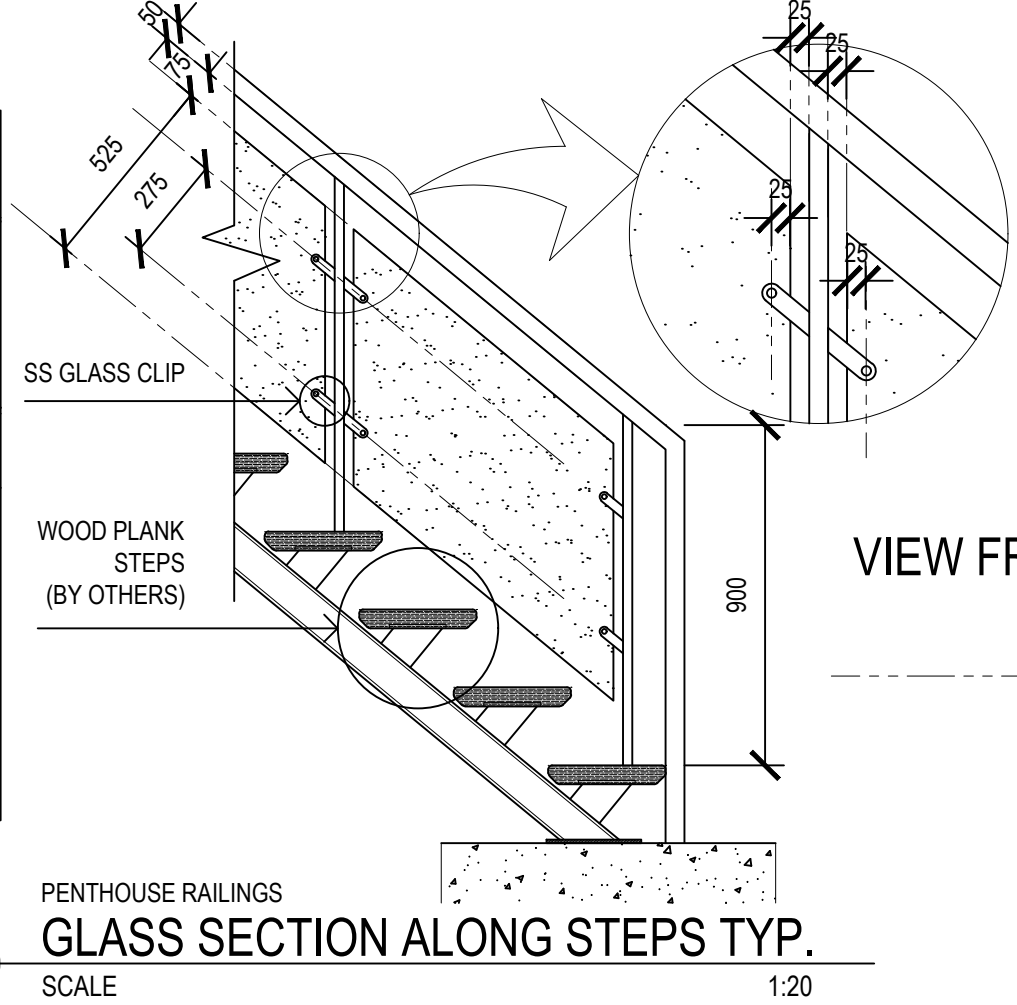


PENTHOUSE RAILINGS
GLASS SECTION ALONG STEPS TYP.
SCALE 1:20

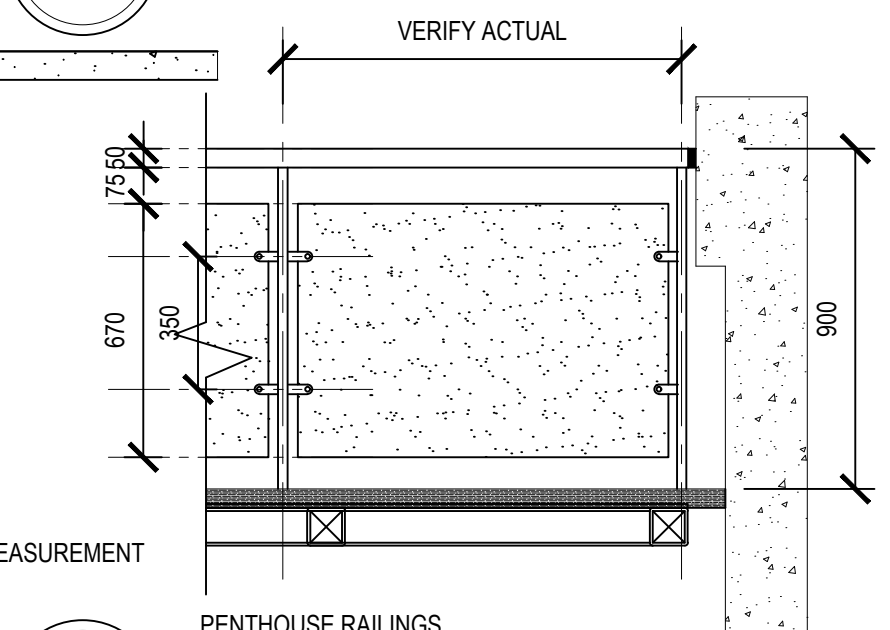

PENTHOUSE RAILINGS
GLASS SECTION AT LANDING TYP.
SCALE 1:20

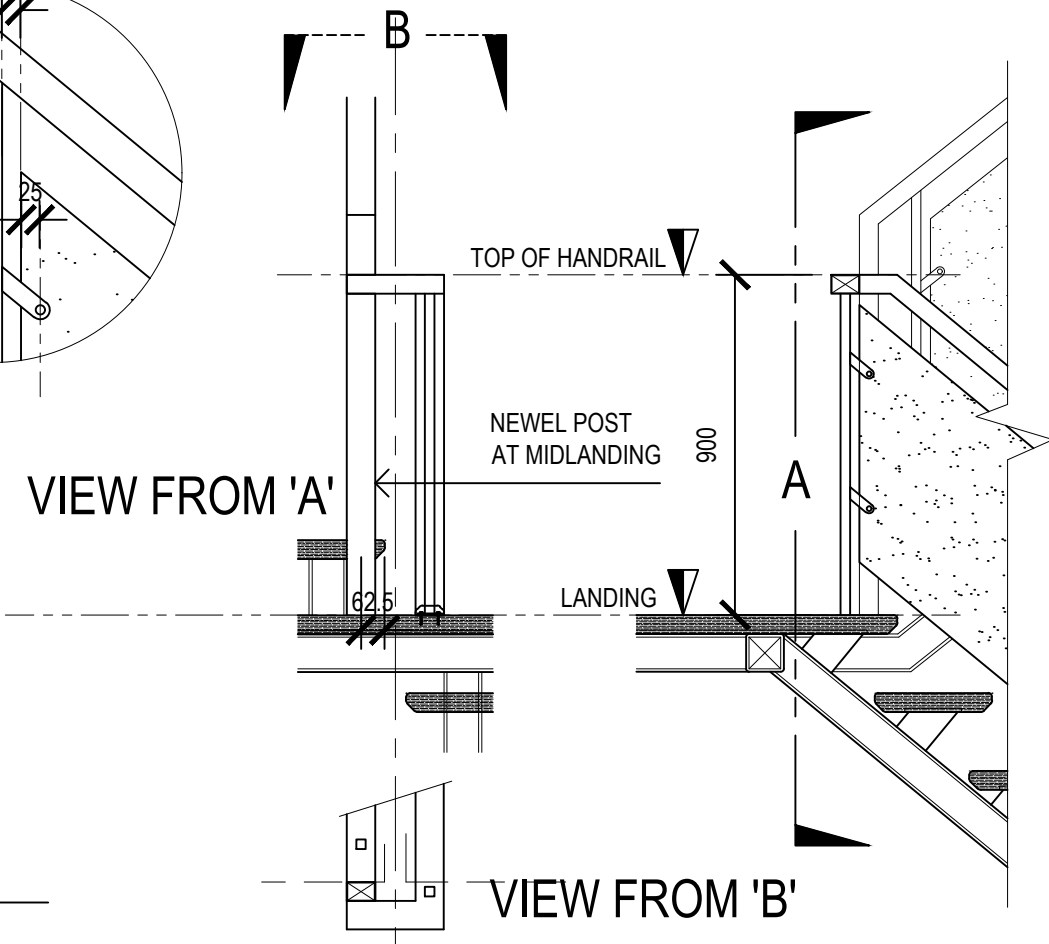

PENTHOUSE RAILINGS
DETAILS AT LANDING
SCALE 1:20

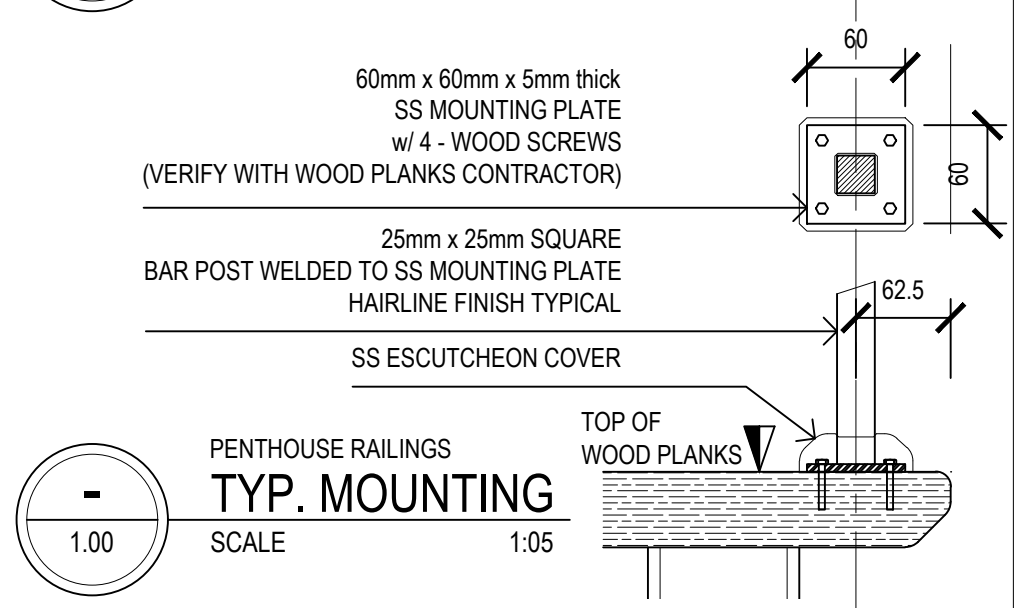

PENTHOUSE RAILINGS
TYP. MOUNTING
SCALE 1:05

- NOTES:
- ALL DIMENSIONS ARE IN MILLIMETERS
 - SUBJECT FOR FINAL SITE INSPECTION AND ACTUAL MEASUREMENT BEFORE FABRICATION
 - GLASS PRODUCTION AND WILL TAKE UP TO 60 TO 80 DAYS UPON CONFIRMED MEASUREMENT AND ORDER.
 - REFERENCE LAYOUT SHOULD BE PROVIDED BY GENERAL CONTRACTOR
 - SQUARE BAR POST SHOULD BE INSTALLED FIRST PRIOR TO GLASS MEASUREMENT

PROJECT TITLE:	OWNER/DEVELOPER:	GENERAL CONTRACTOR:	SHEET CONTENT:	SHEET NUMBER:
			STAIR GLASS RAILINGS	1.00
			REMARKS:	REVISION: 0.0