

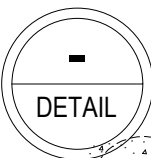


- NOTES:
- 1. ALL DIMENSIONS ARE IN MILLIMETERS
 - 2. SUBJECT FOR FINAL SITE INSPECTION AND ACTUAL MEASUREMENT BEFORE FABRICATION
 - 3. ALL LOUVER PANELS WILL UNDERGO GALVANIZING PRIOR TO EPOXY PRIMER APPLICATION


M12 x 140 FISCHER CHEMBOLT
TYPICAL TO ALL CONNECTIONS
(110mm EMBEDMENT DEPTH ~ FOR APPROVAL)

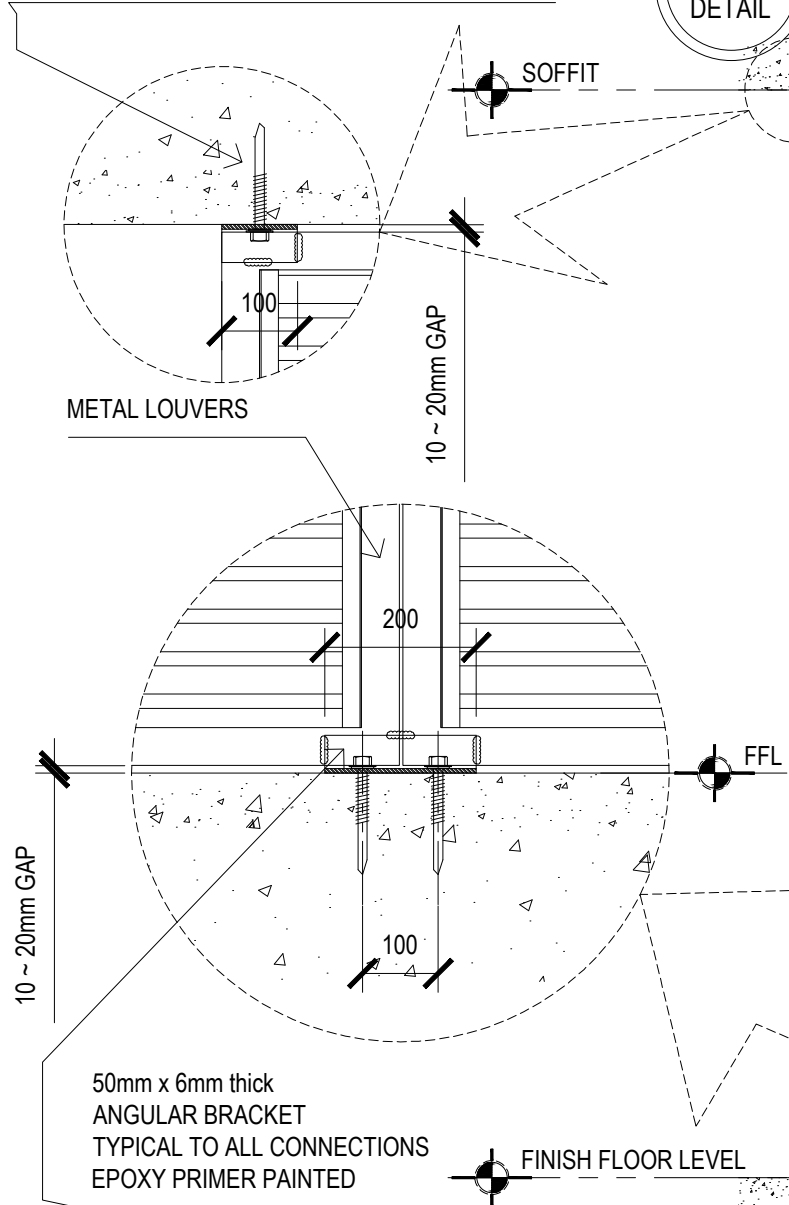

METAL LOUVERS
TYP. PLAN
SCALE 1:30


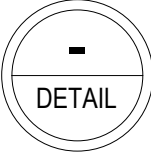


METAL LOUVERS
TYP. ELEVATION
SCALE 1:30

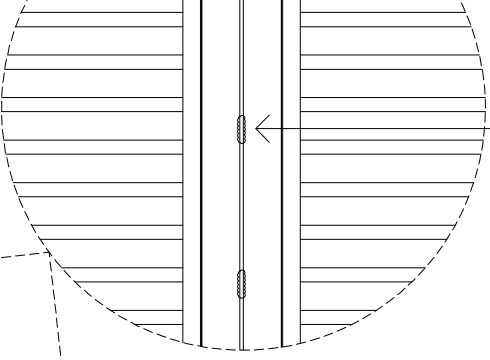

INTERMITTENT WELDING JOINTS
MAX SPACING IS 500mm

FINAL SETTING OUT
BY MDC

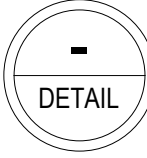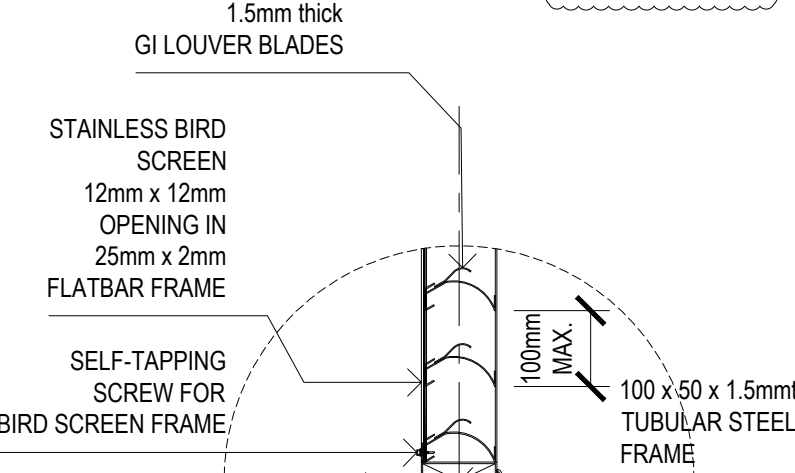

METAL LOUVERS
TYP. SECTION
SCALE 1:30

PROJECT TITLE:	OWNER/DEVELOPER:	GENERAL CONTRACTOR:	SHEET CONTENT:	SHEET NUMBER:
			DETAIL SHEET	DETAIL
			REMARKS:	REVISION: 0.00