


50 X 10T SS FLATBAR FRAME
W/ Ø8MM X 75MM SS EXPANSION BOLT
AT EVERY 900MM O.C.

3/4"Ø SS ROUND BAR
STEPS AT
EVERY 300MM O.C.

ISOMETRIC

- NOTE:
- 1. ALL DIMENSIONS ARE IN MILLIMETERS
 - 2. SUBJECT FOR FINAL SITE INSPECTION AND ACTUAL MEASUREMENT BEFORE FABRICATION
 - 3. ALL MEMBERS ARE STAINLESS

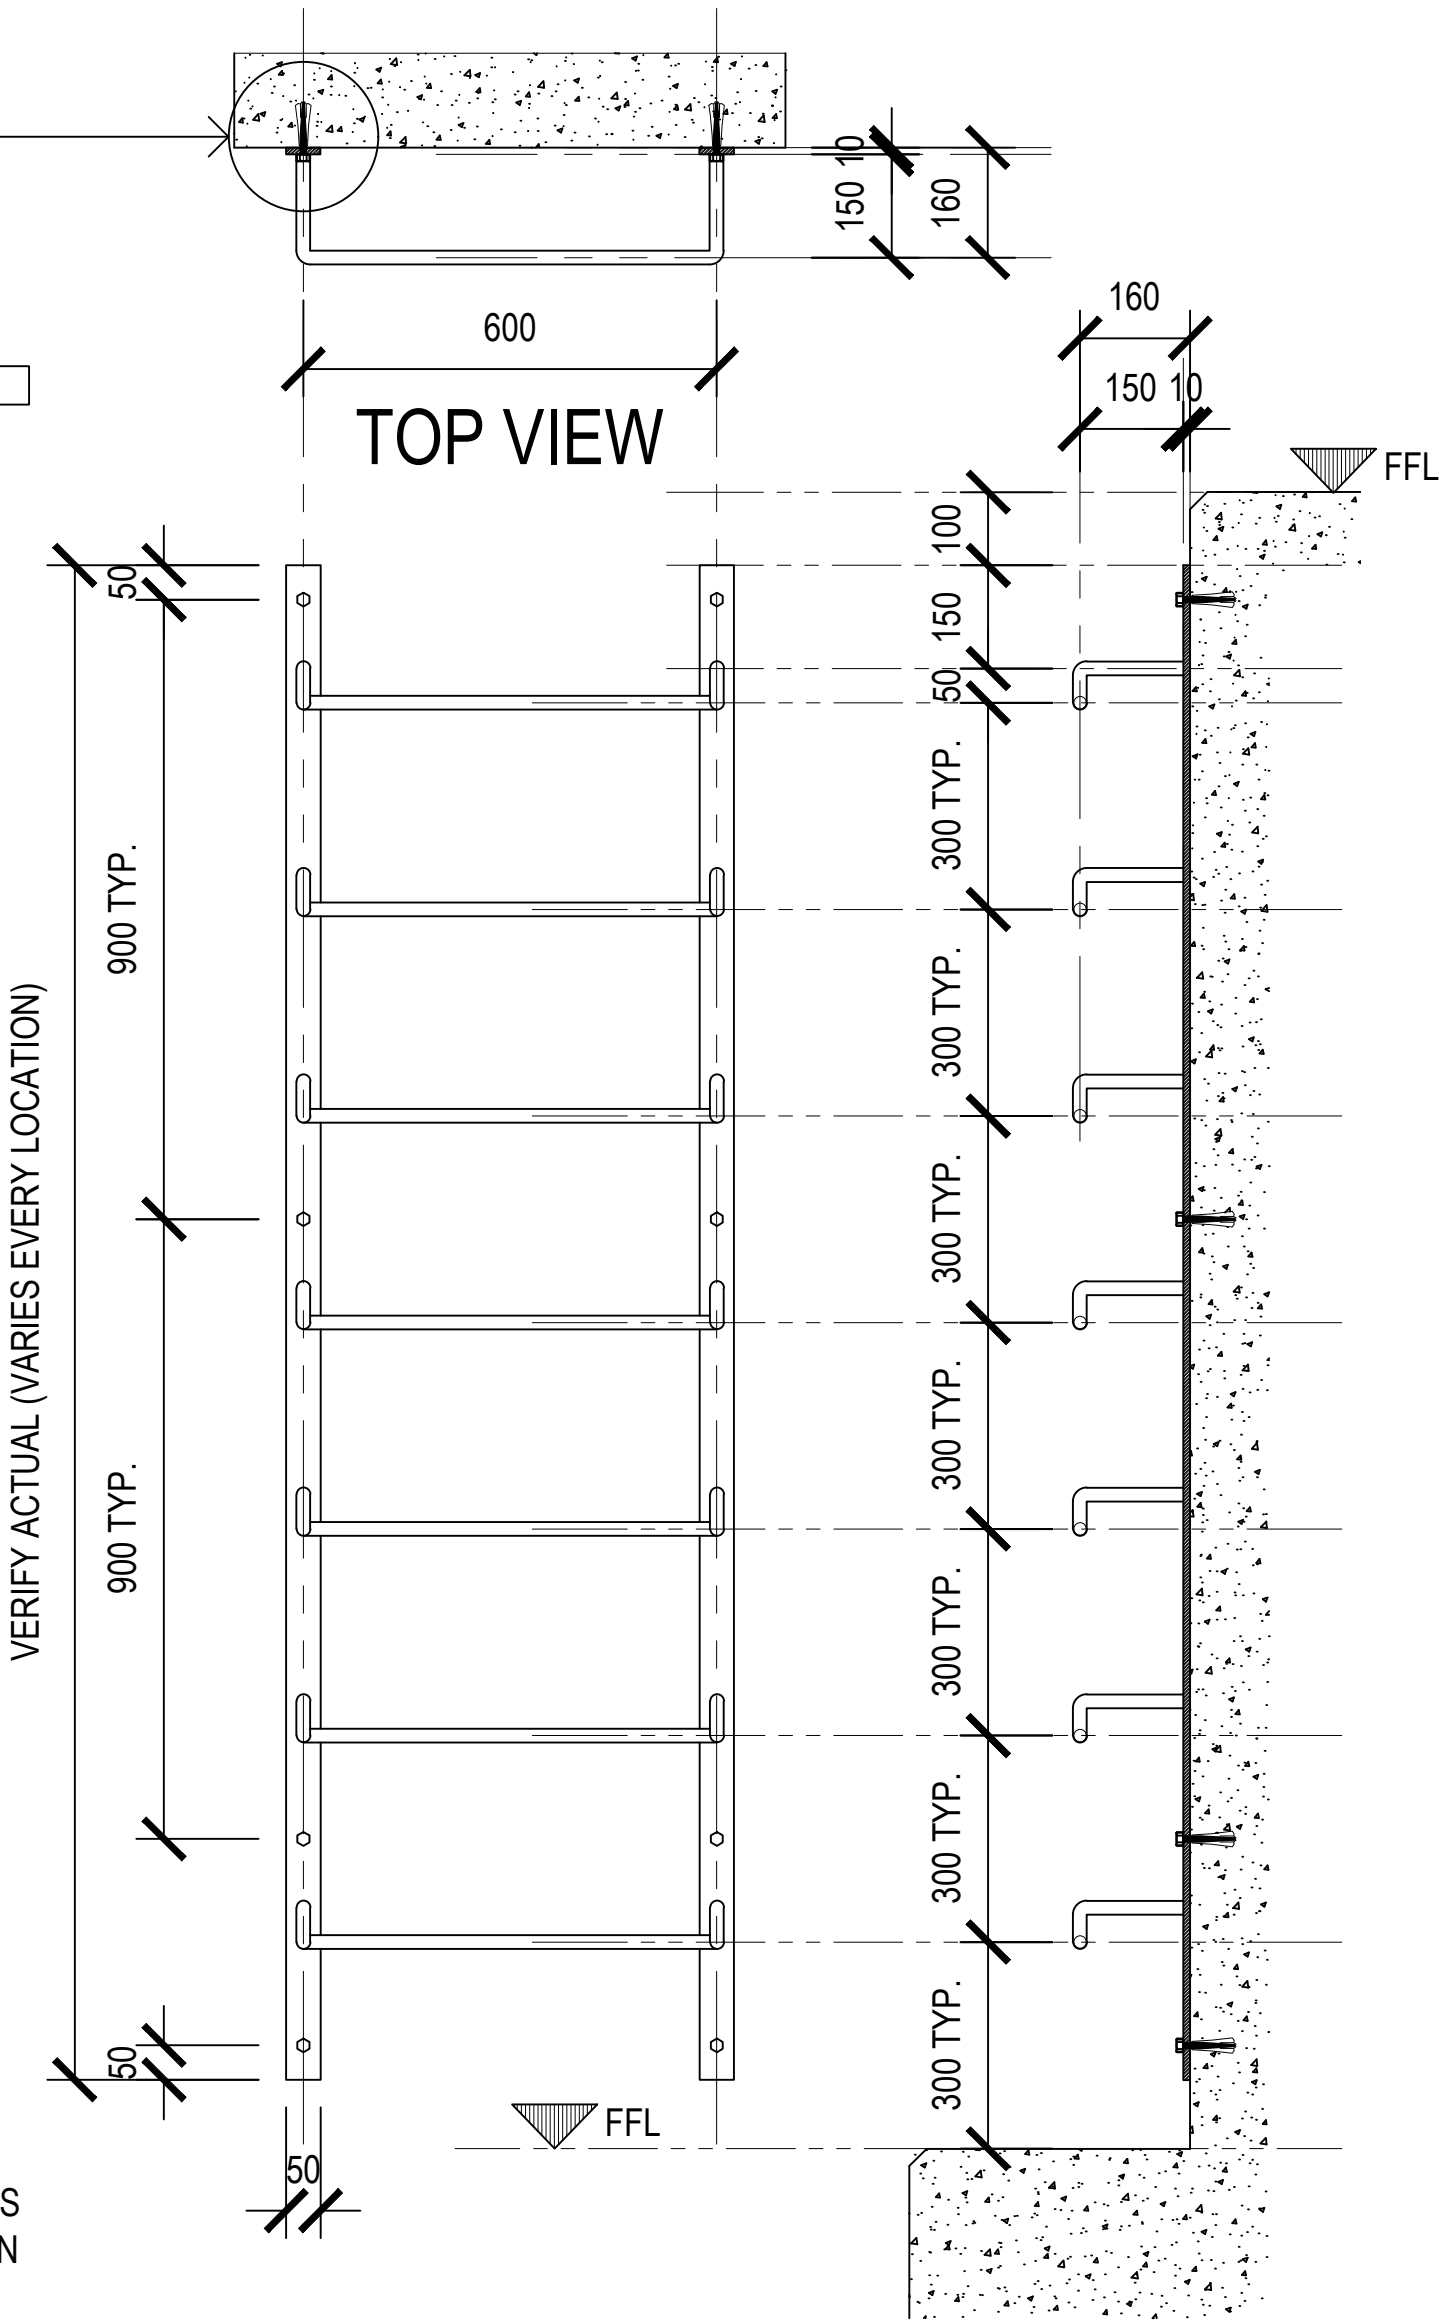

PROJECT TITLE:	SHEET CONTENT:	SHEET NO. :
	LADDER RUNG DETAILS	1.00
		REVISION 0.0