
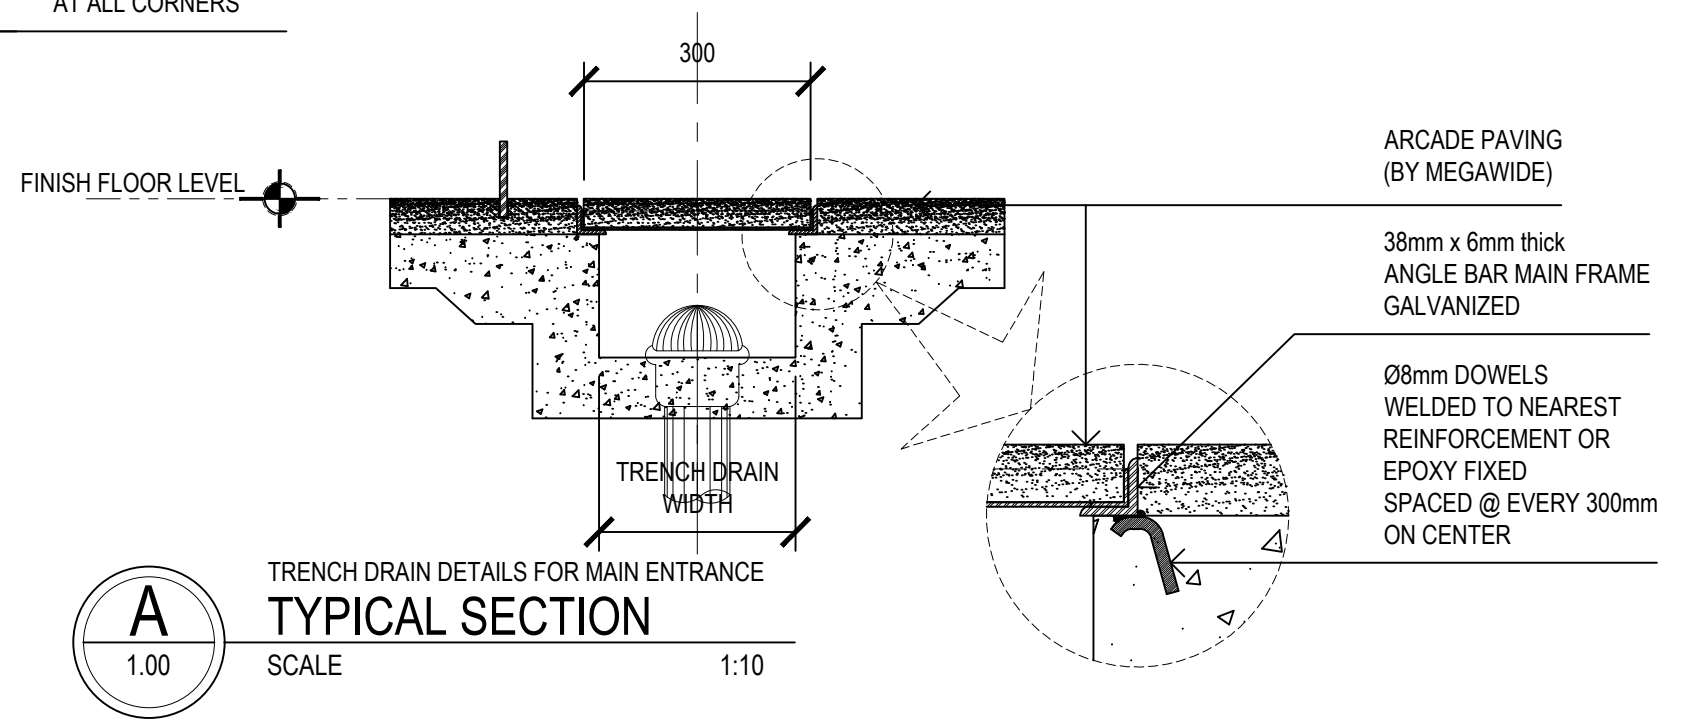
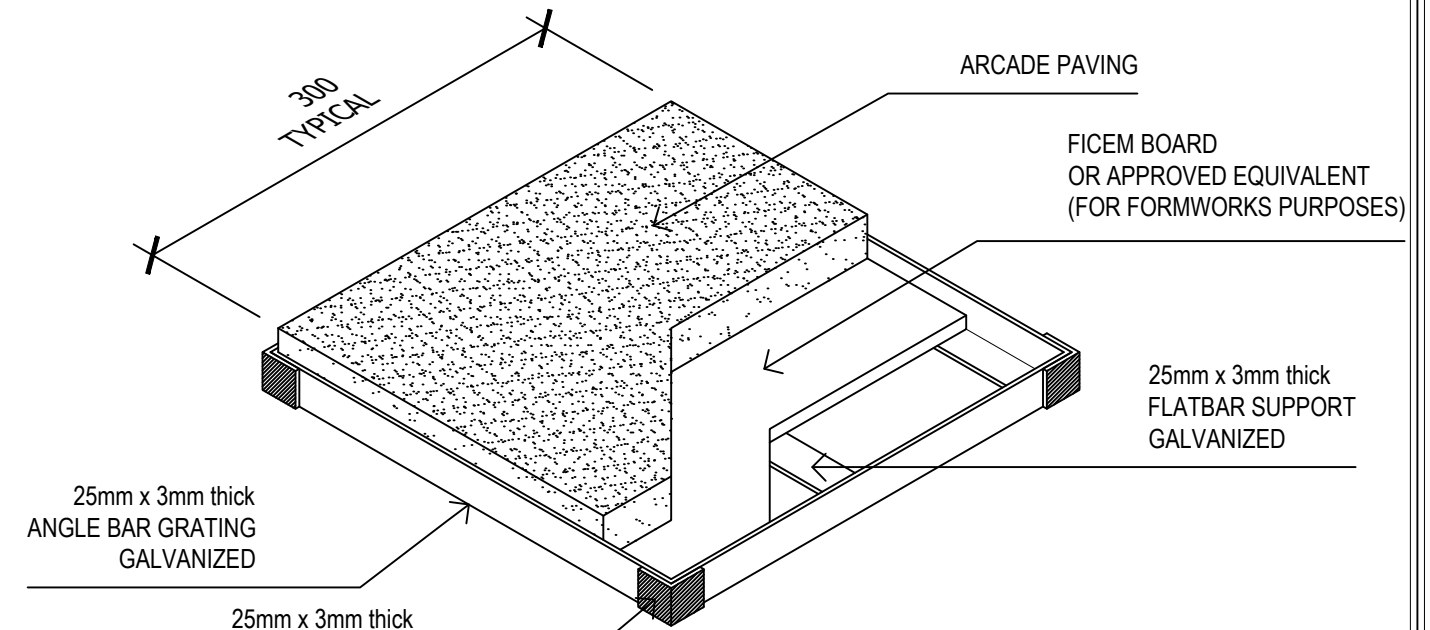


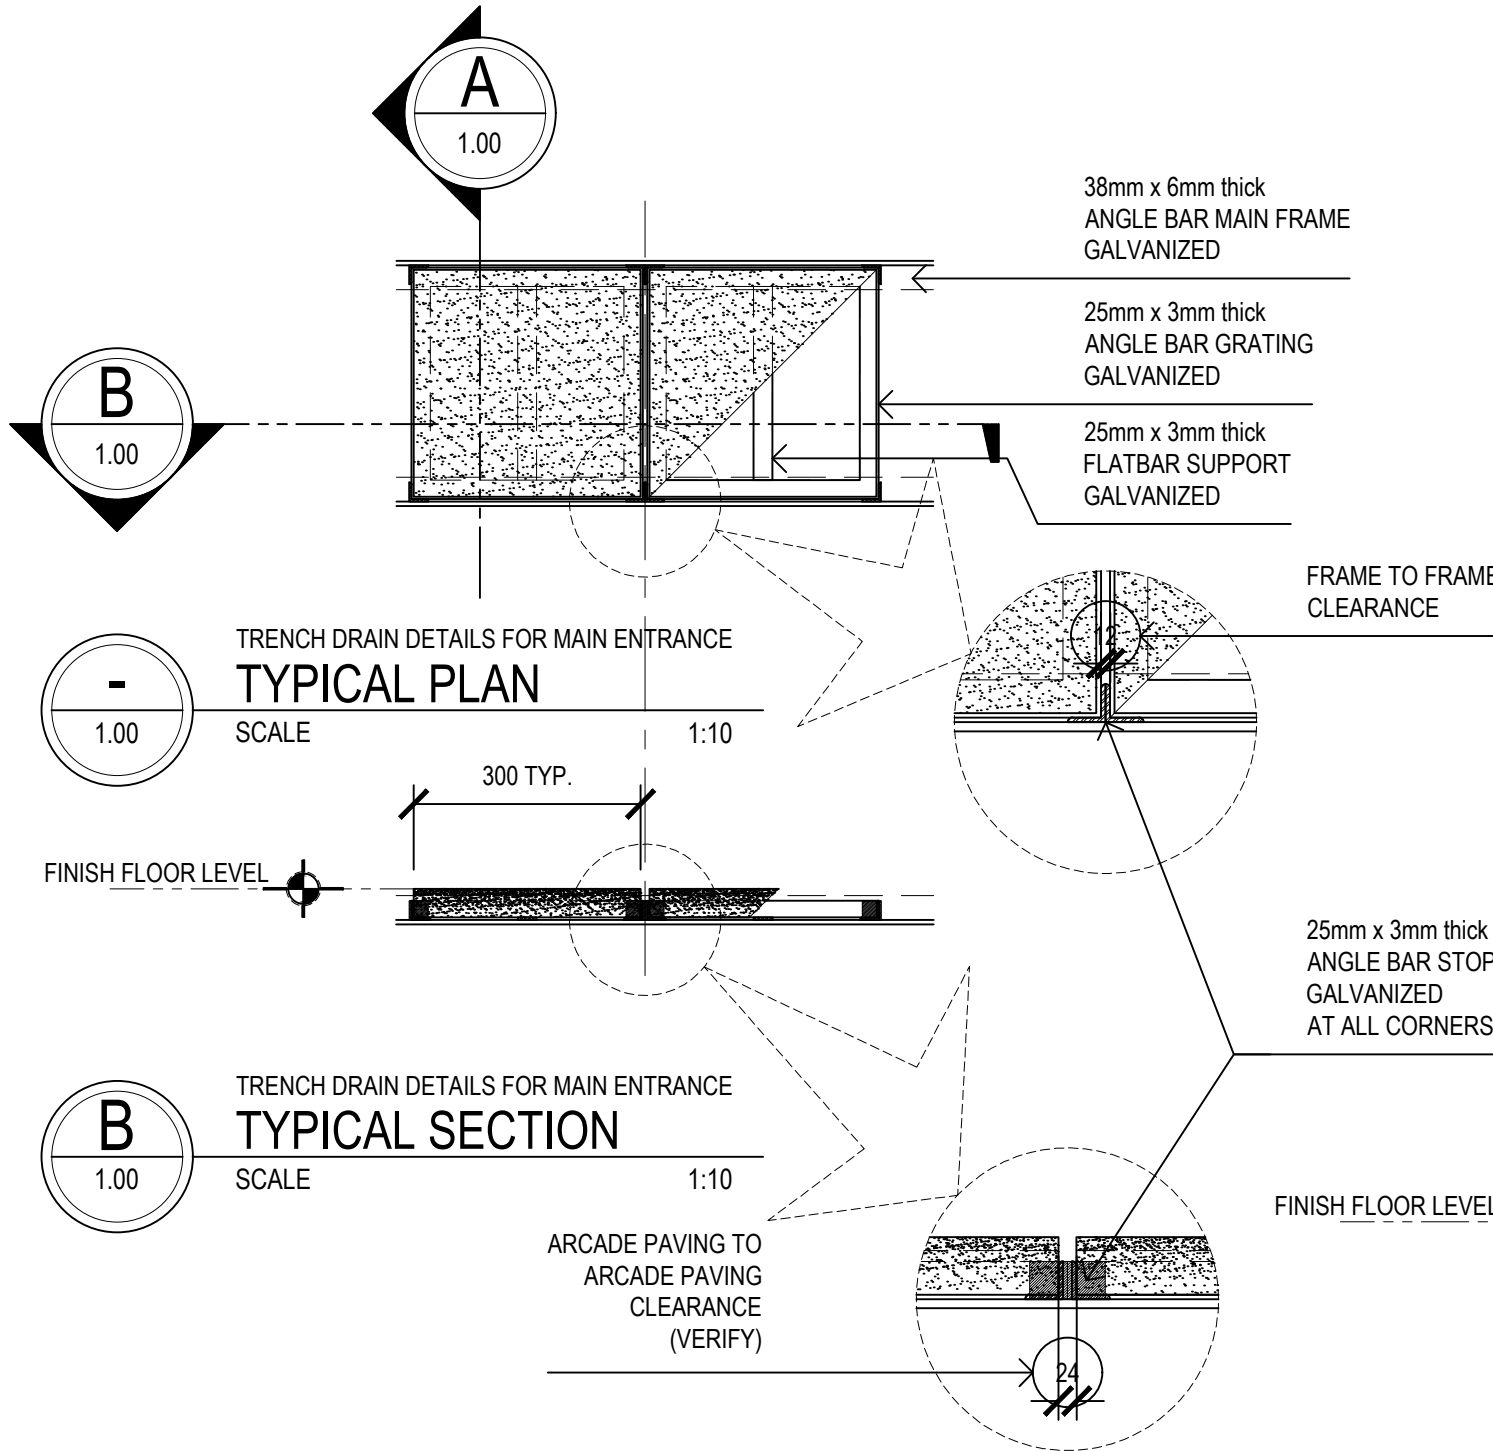

- NOTES:
1. ALL DIMENSIONS ARE IN MILLIMETERS
SUBJECT FOR FINAL SITE INSPECTION
AND ACTUAL MEASUREMENT BEFORE
FABRICATION
 2. ALL ANGULAR AND FLATBAR MEMBERS
ARE IN GALVANIZED FINISH

PROJECT TITLE:	OWNER/DEVELOPER:	GENERAL CONTRACTOR:	SHEET CONTENT:	SHEET NUMBER:
			TRENCH DRAIN DETAILS FOR MAIN ENTRANCE	1.00
			REMARKS:	REVISION: 0.00