


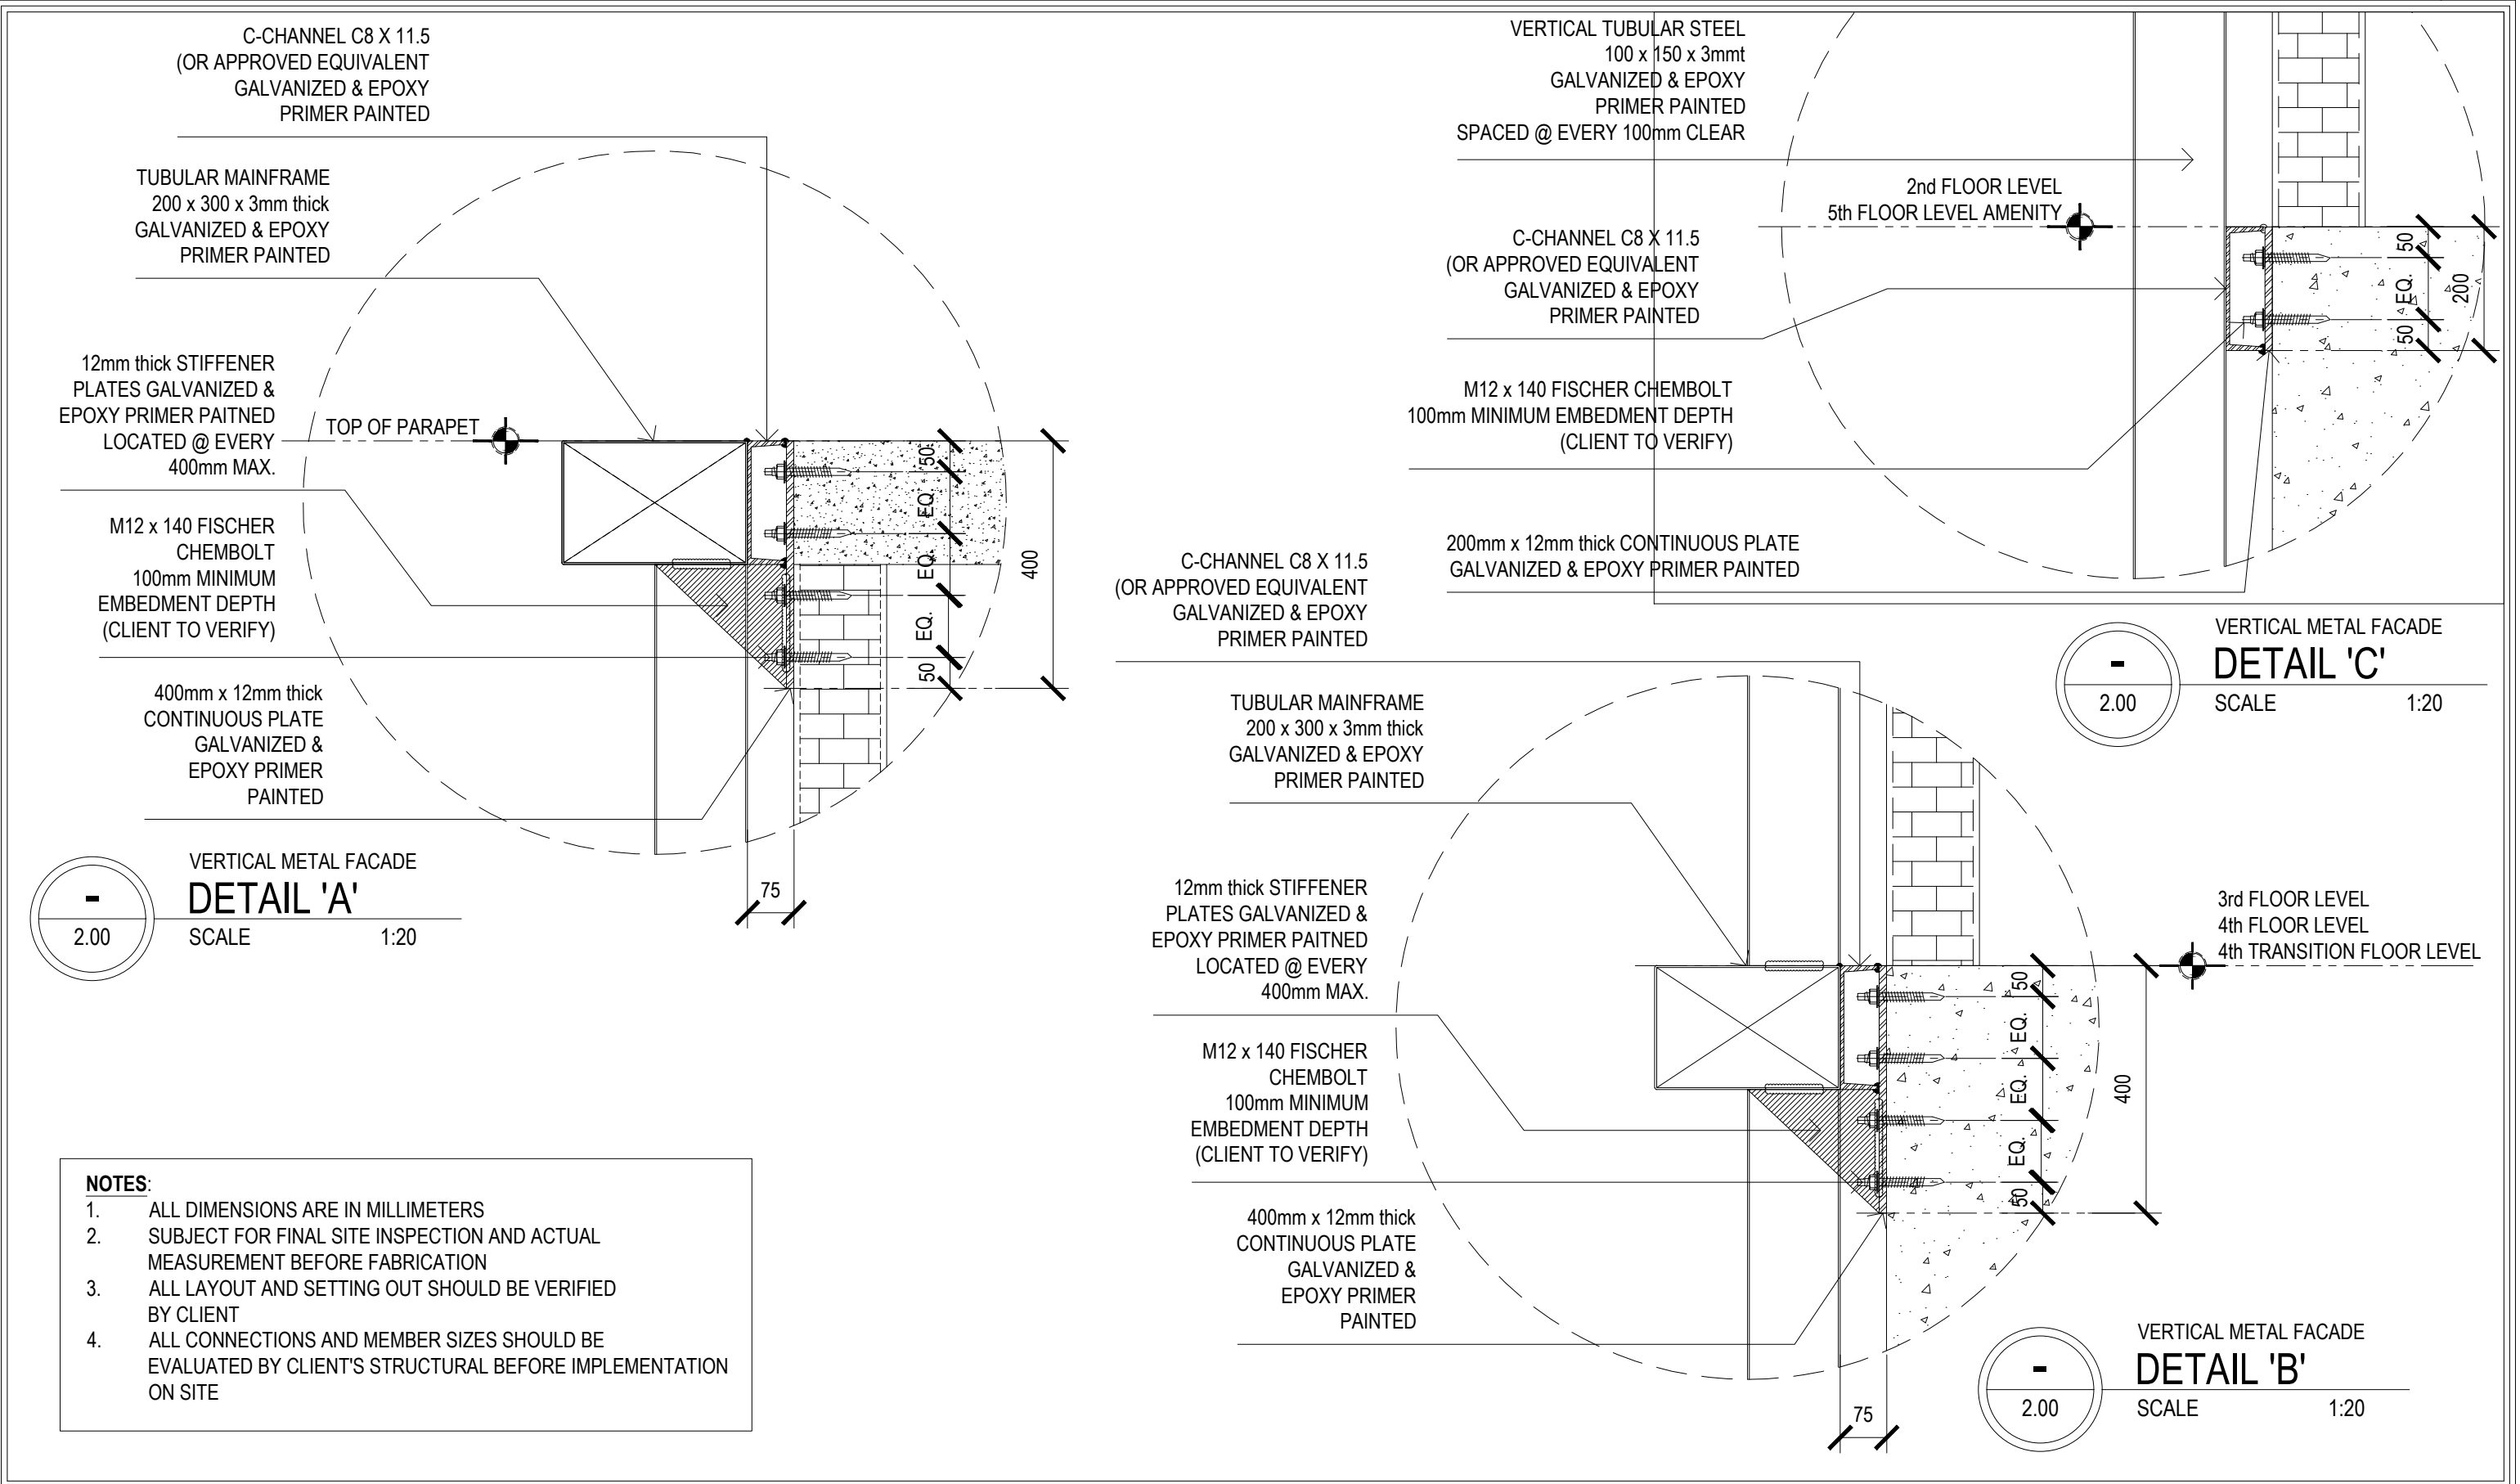

	PROJECT TITLE:	OWNER/DEVELOPER:	GENERAL CONTRACTOR:	SHEET CONTENT:	SHEET NUMBER:
				VERTICAL METAL FACADE CONNECTION DETAILS	2.00
				REMARKS:	REVISION: 0.00