




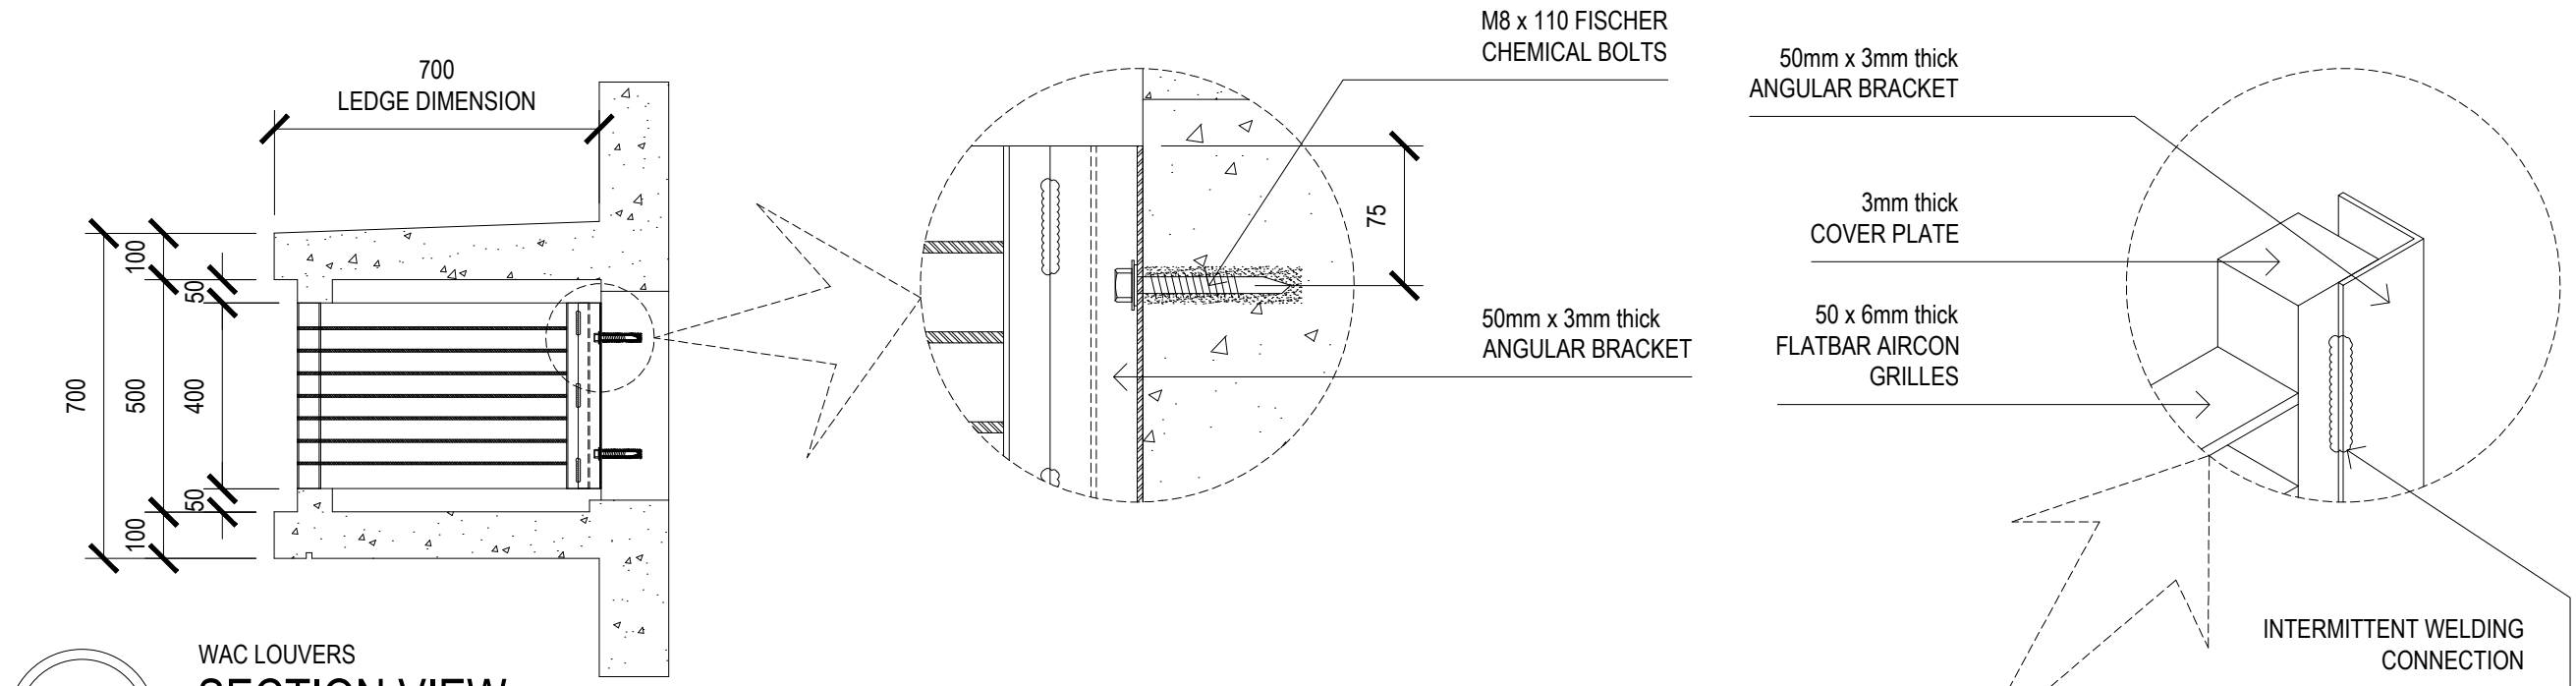

WAC LOUVERS
SECTION VIEW
SCALE 1:16

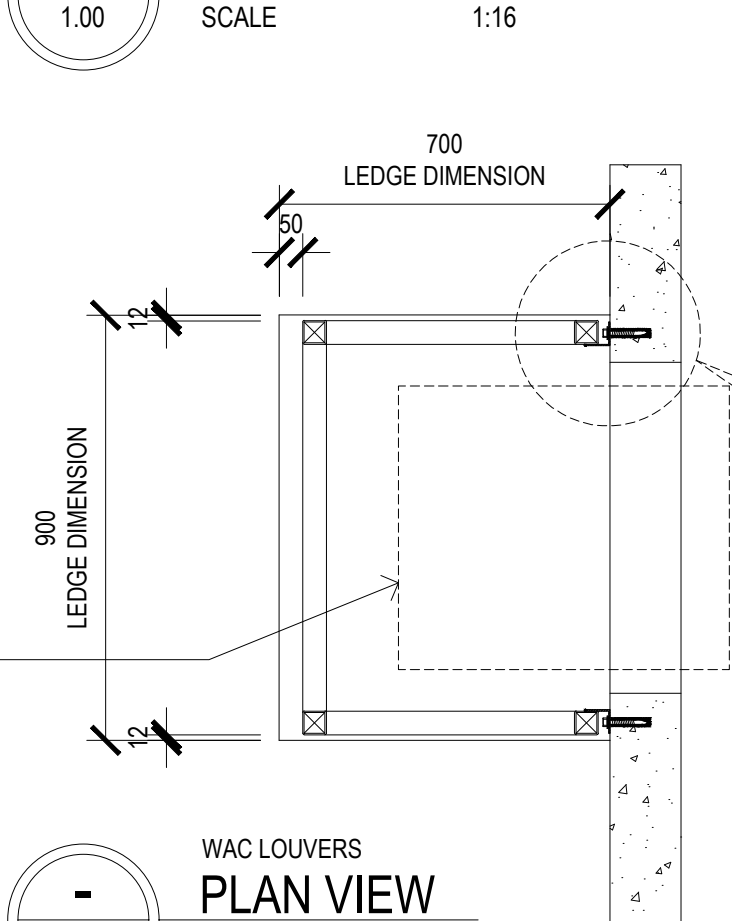

WAC LOUVERS
PLAN VIEW
SCALE 1:16

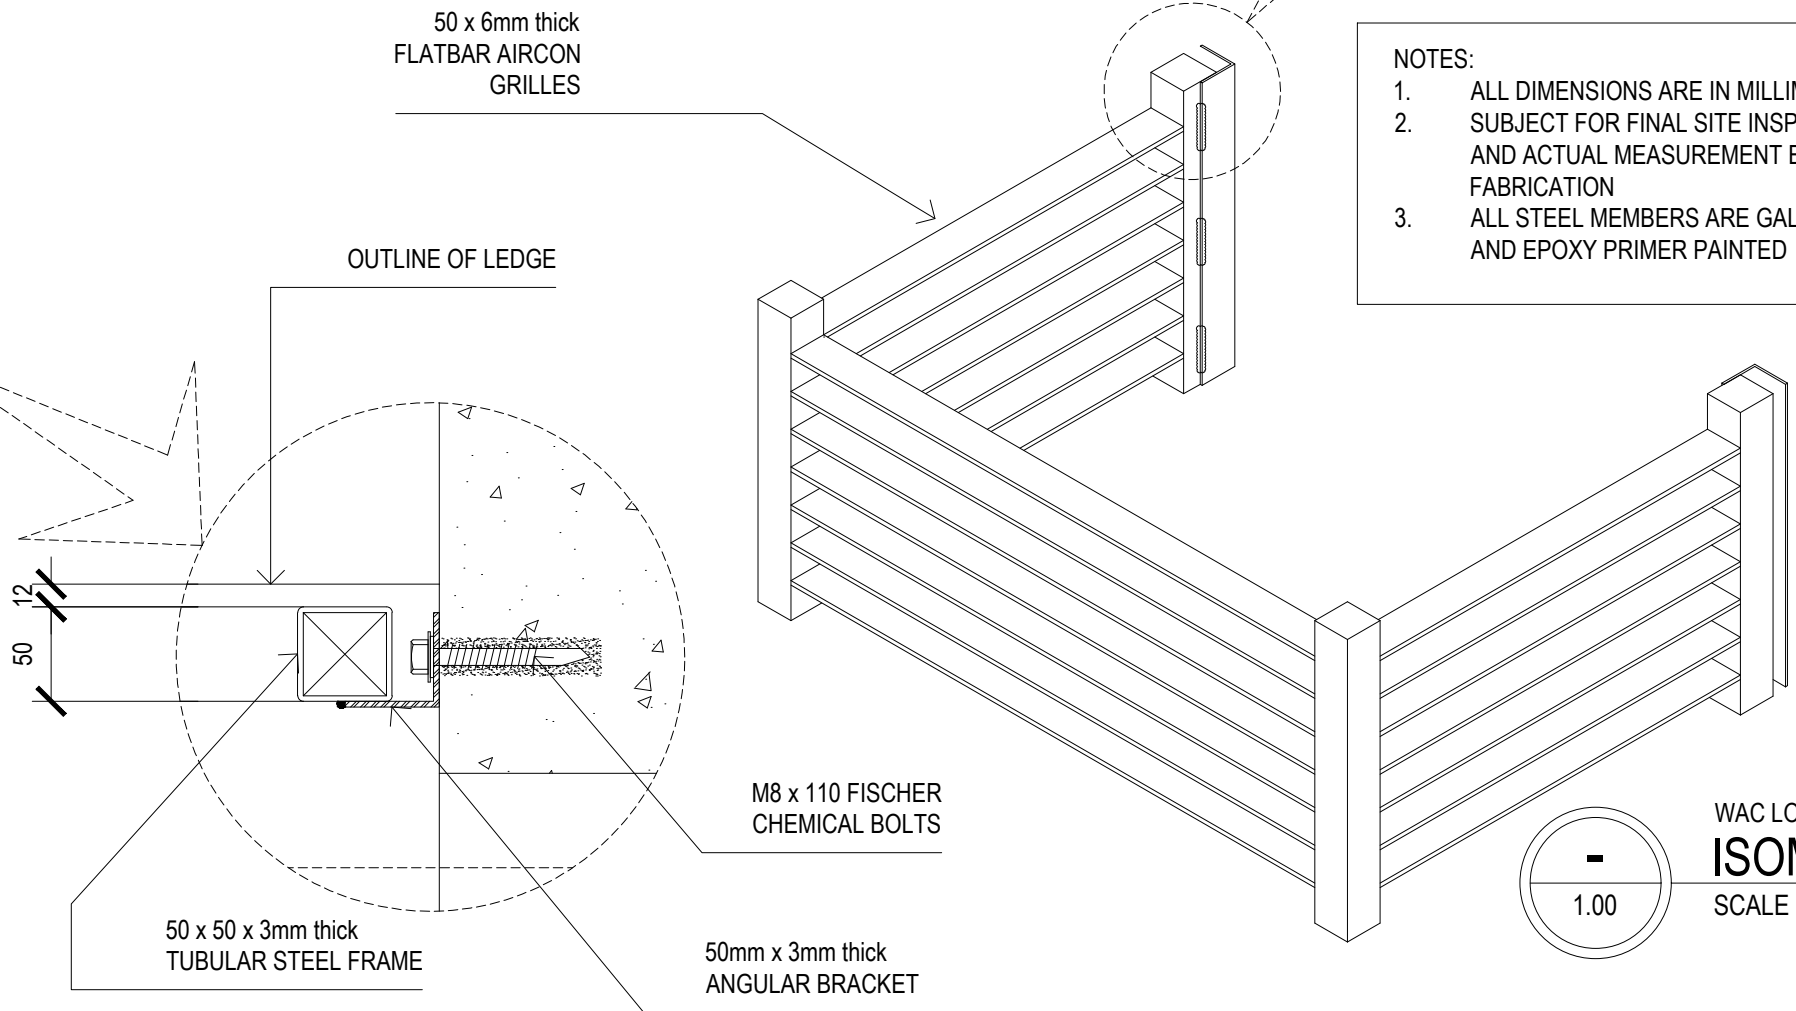

- NOTES:
1. ALL DIMENSIONS ARE IN MILLIMETERS
 2. SUBJECT FOR FINAL SITE INSPECTION AND ACTUAL MEASUREMENT BEFORE FABRICATION
 3. ALL STEEL MEMBERS ARE GALVANIZED AND EPOXY PRIMER PAINTED

WAC LOUVERS
ISOMETRIC
SCALE 1:10

	PROJECT TITLE:	OWNER/DEVELOPER:	GENERAL CONTRACTOR:	SHEET CONTENT:	SHEET NUMBER:
				TYPICAL DETAILS OF WAC LOUVERS	1.00
				REMARKS:	REVISION: 0.00