

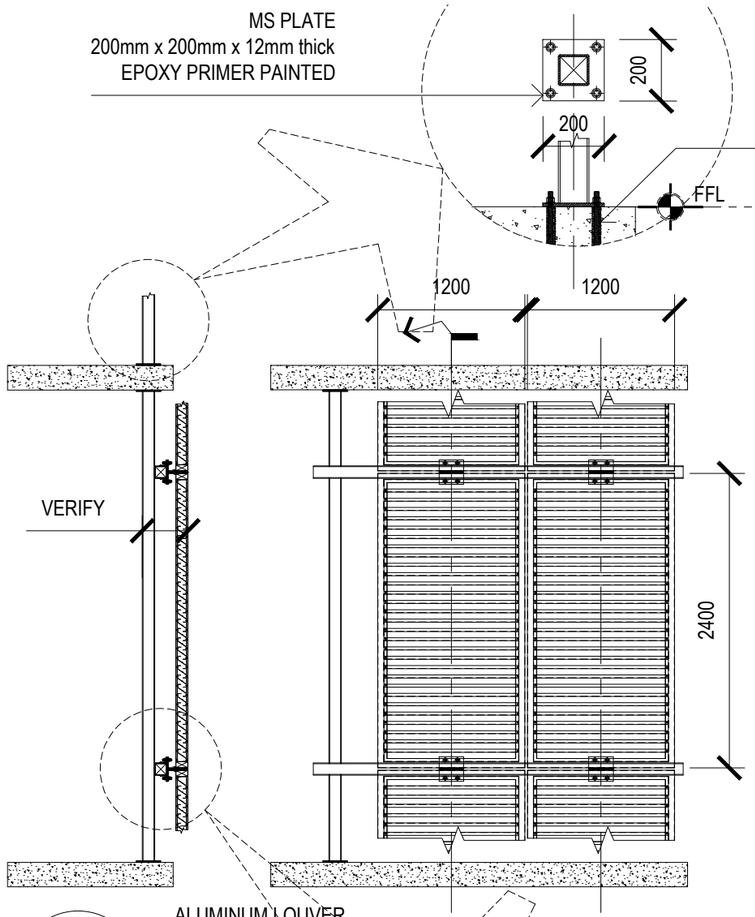


ALUMINUM LOUVER

TYP. ELEVATION & SECTION

6.00 SCALE 1:50

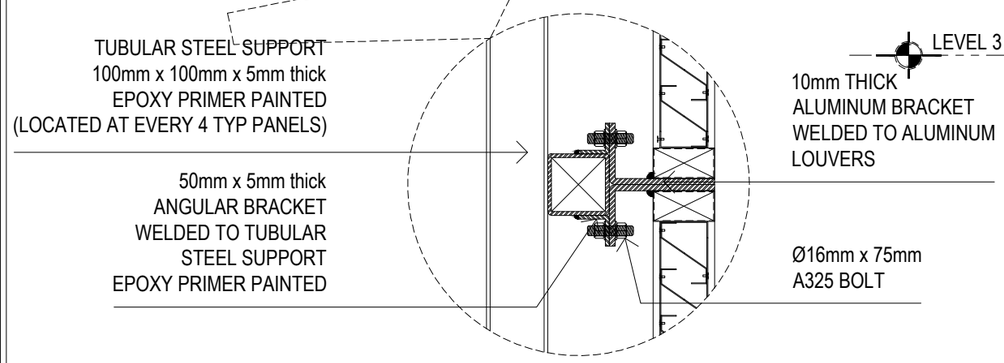

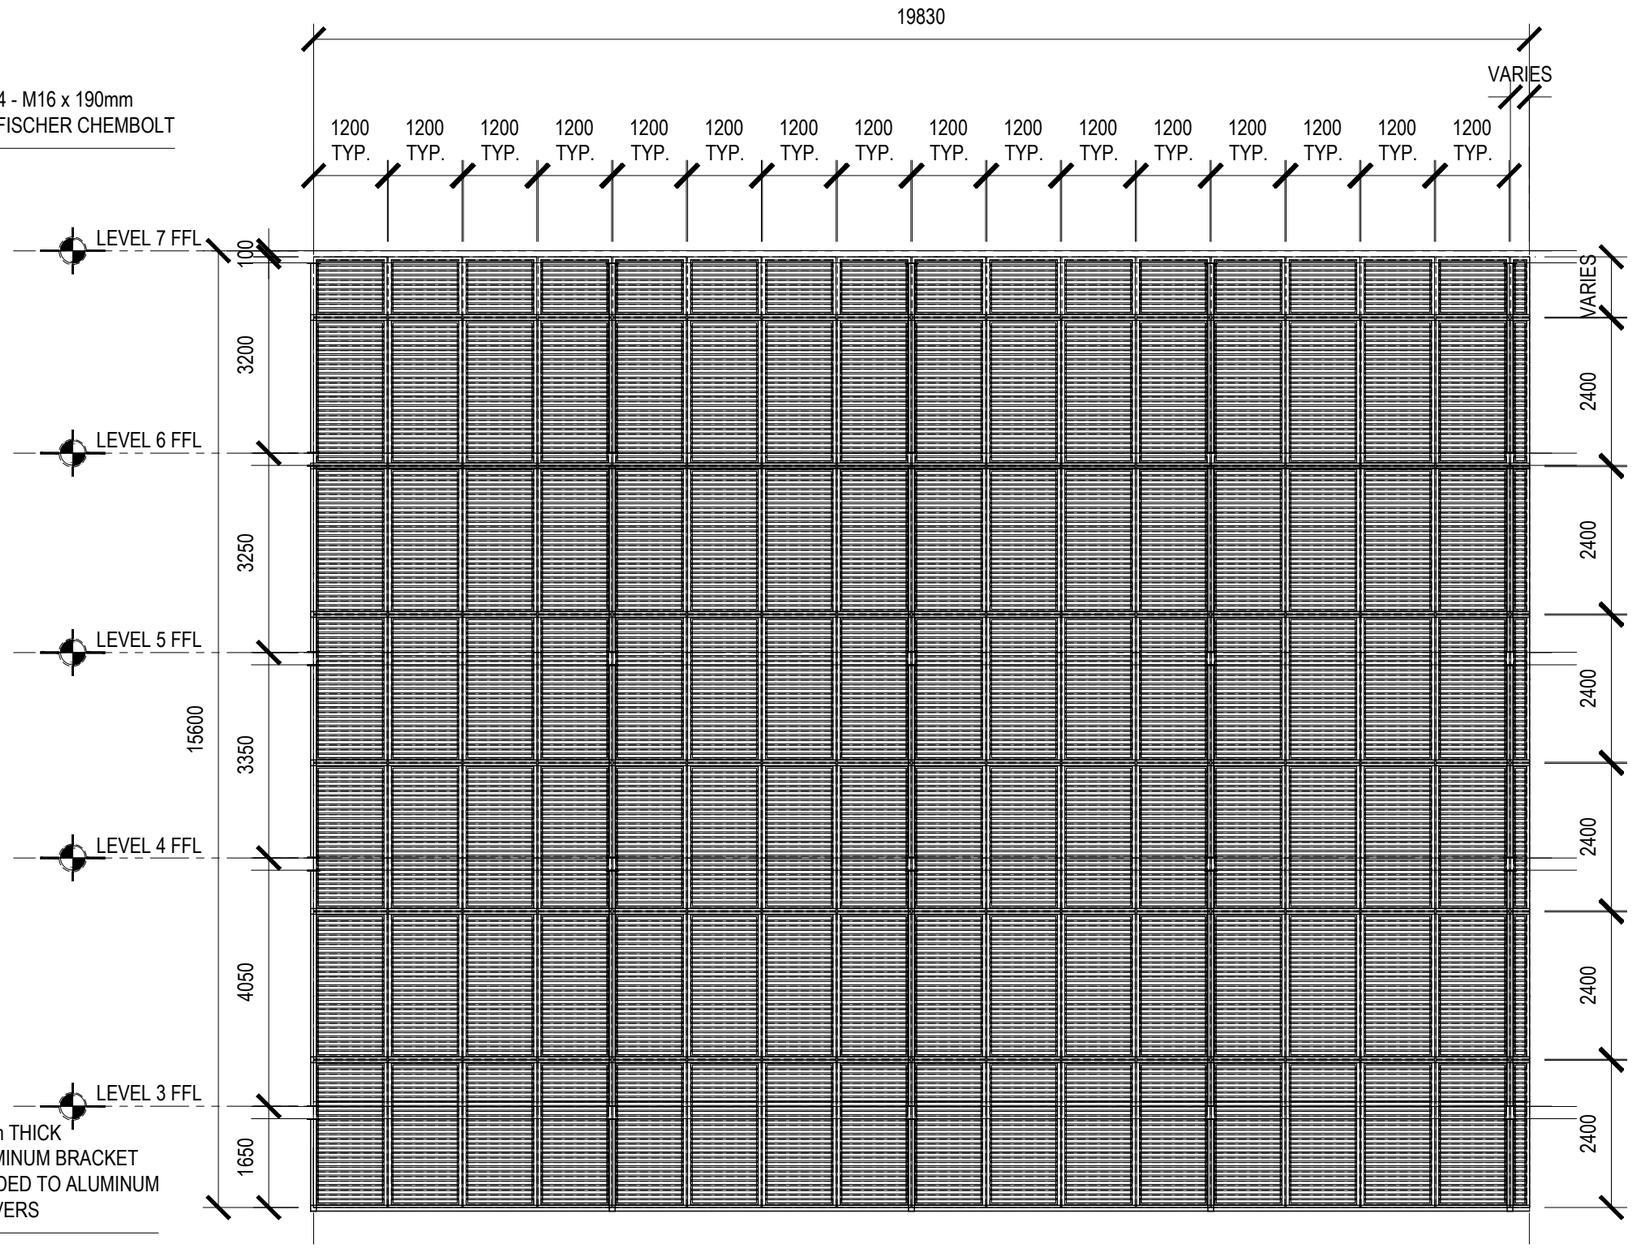

ALUMINUM LOUVER

LOUVER SCHEDULE : L-13

6.00 SCALE 1:100

PROJECT TITLE:	OWNER/DEVELOPER:	GENERAL CONTRACTOR:	SHEET CONTENT:	SHEET NUMBER:
			ALUMINUM LOUVER DETAILS	6.00
			REMARKS:	REVISION: 0.0